


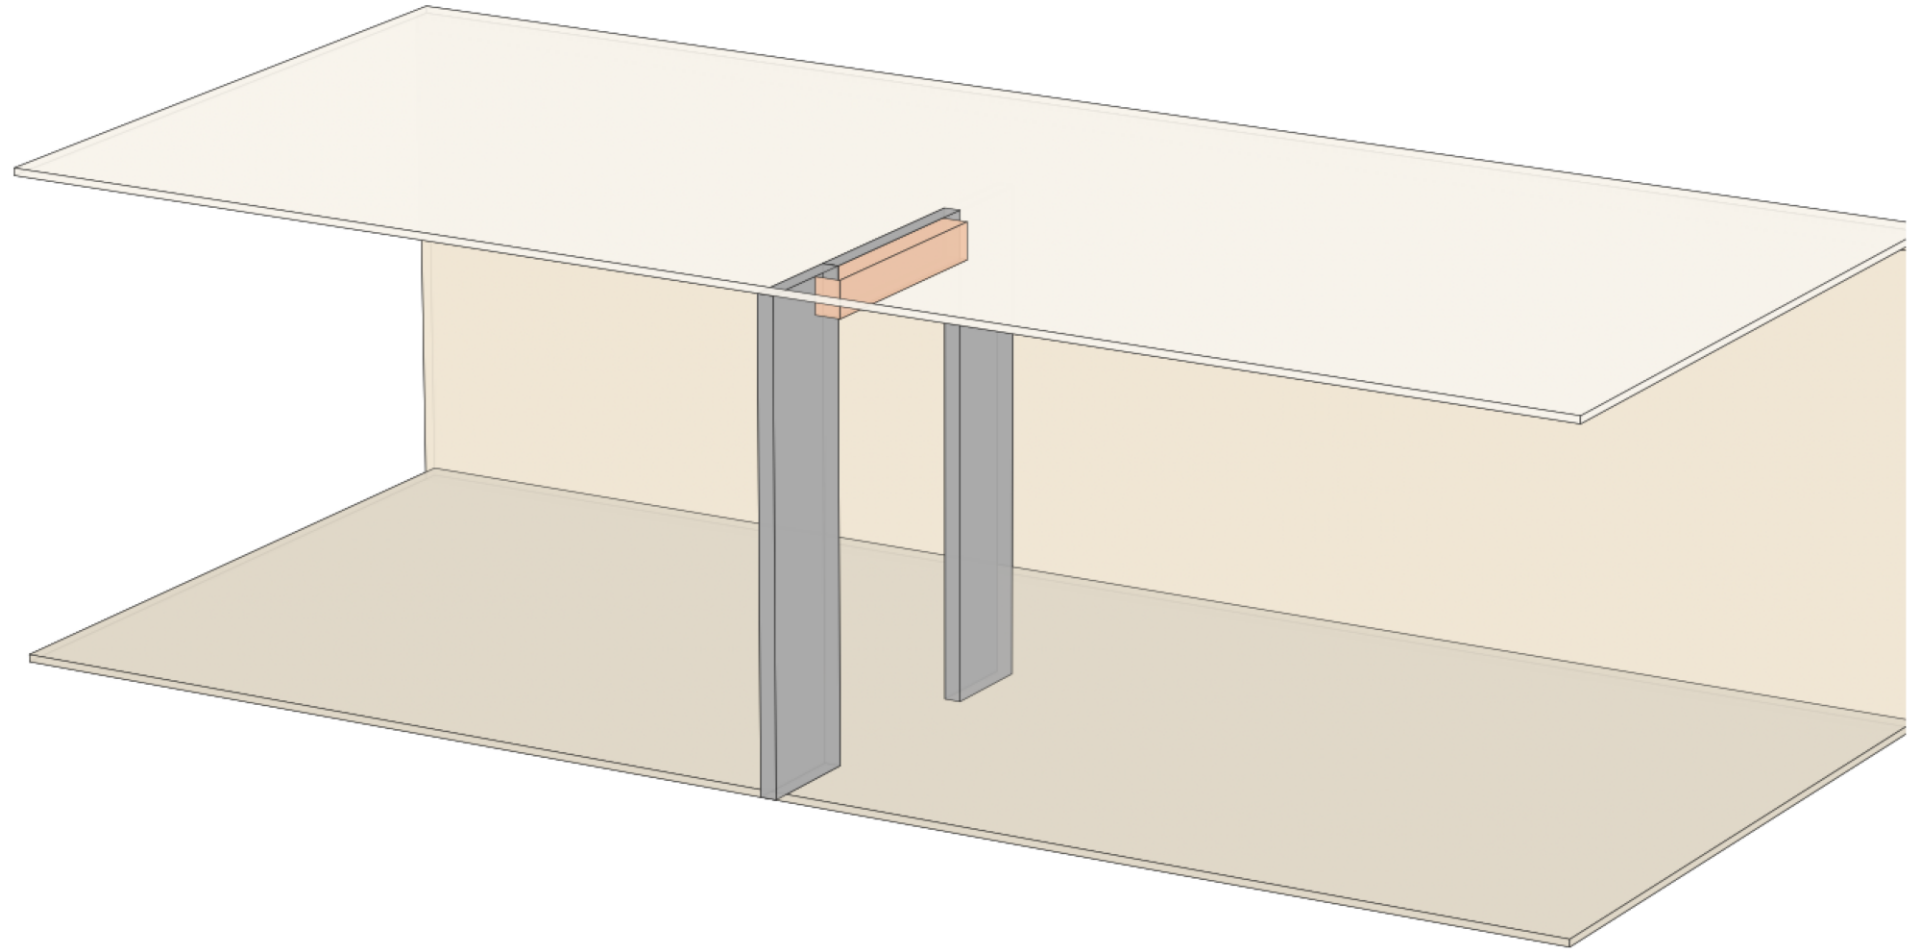

OPENING — between front lounge & rear reception

- Clear width: 1350 mm
- Clear height: 2950 mm
- Nib L / nib R: 700 / 600 mm
- Beam zone (orange): ~250 mm deep
(final size by engineer)

MAKING GOOD

- Plaster reveal both sides — match existing finishes.
- Skirting returns into nibs.
- Cornice cut & profiled at heads — re-run matching profile across the new opening.

PROJECT	Flat 1, 20 Hornton Street, London W8 4NR	SCALE	1:1 @ A3
DRAWING TITLE	3D AXONOMETRIC — Proposed internal opening (rec rooms)	DRAWING NO.	12
CLIENT	Grahame McGirr	DATE	2026-05-25
REVISION	B	SHEET SIZE	A3 (420 x 297)
UNITS	All dimensions in millimetres (mm)	STATUS	FOR PLANNING