

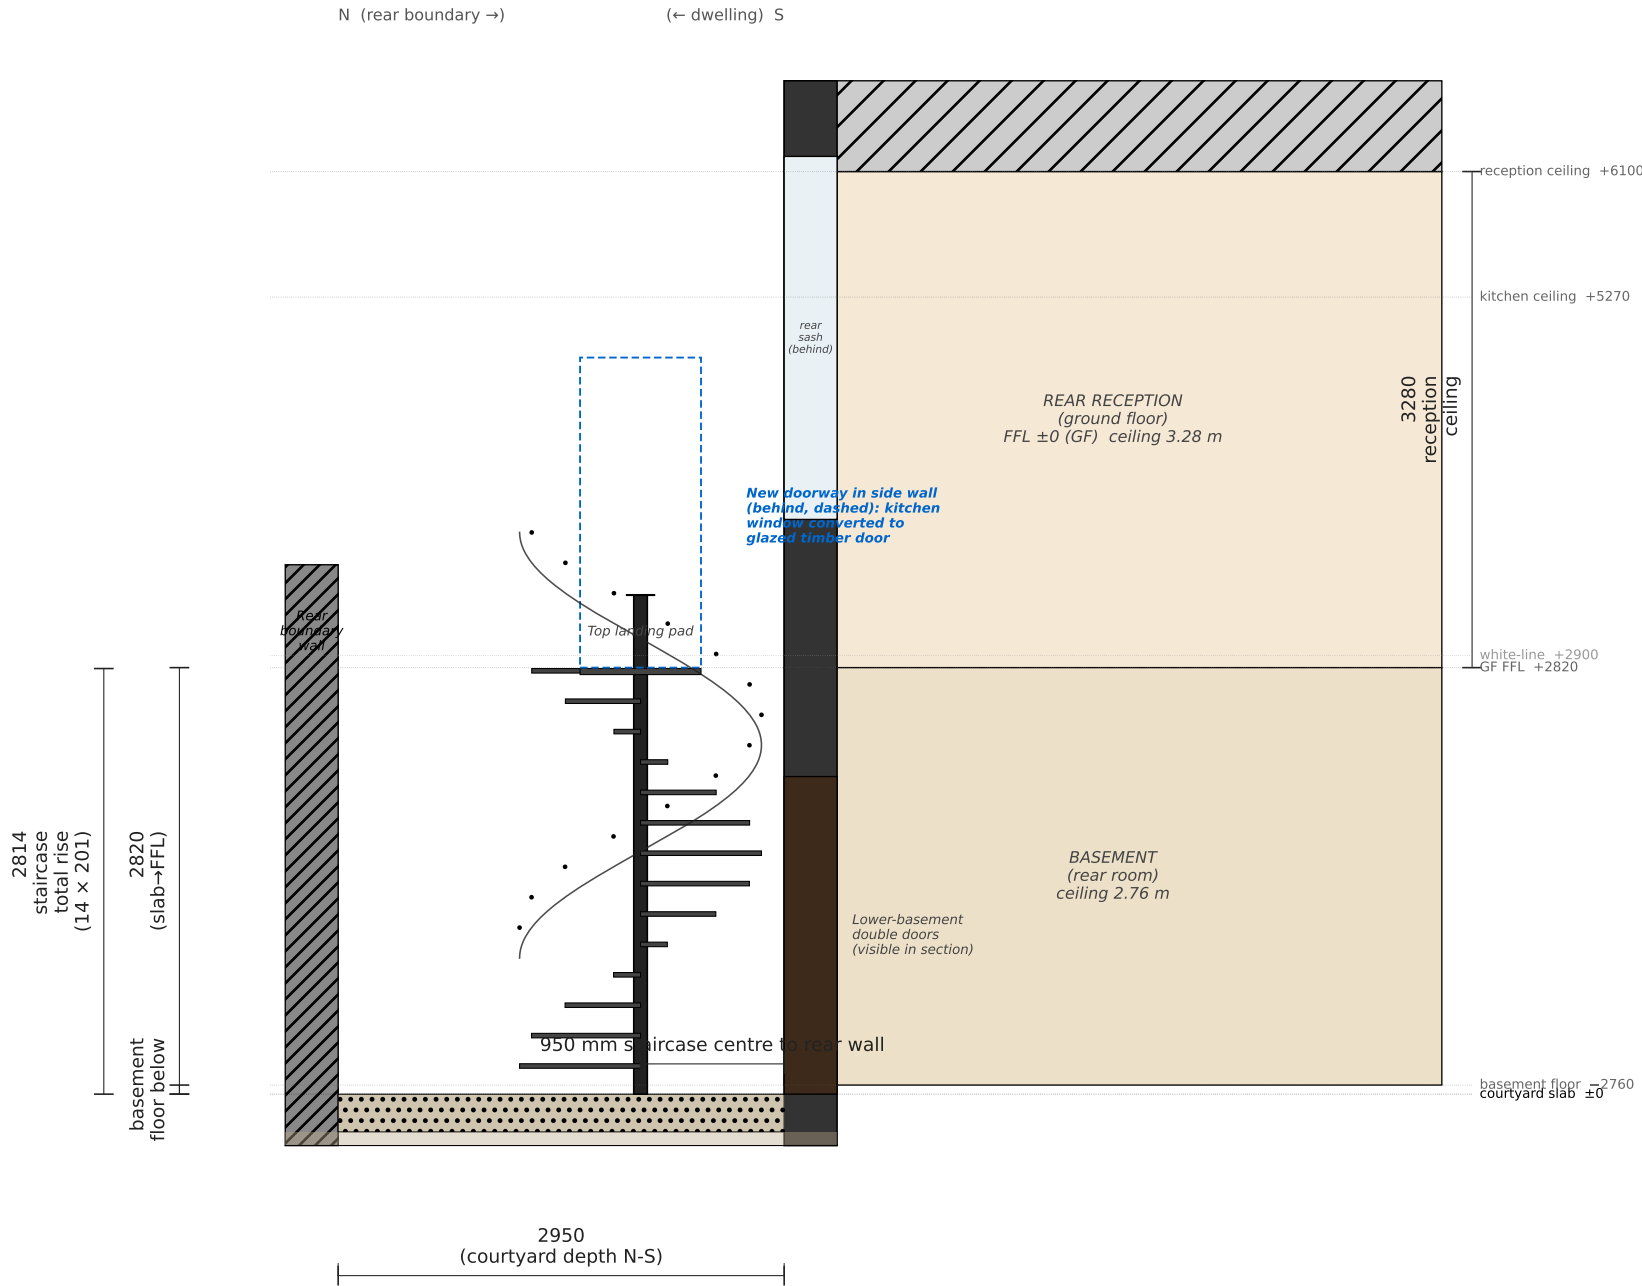


SECTION A-A — through centre of spiral staircase, looking WEST

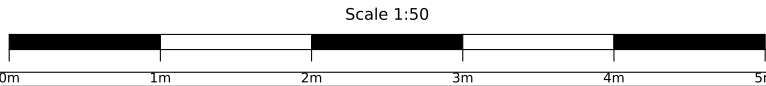

NOTES — COURTYARD SECTION A-A

- Cut: N-S through centre of proposed spiral staircase, viewer looking WEST.
- Rear-reception room (south) and basement room shown to the right of section.
- Rear boundary wall (north) shown to the left.
- Datums:
 - Courtyard slab = ±0
 - Basement floor = -2760
 - Ground floor FFL = +2820
 - Kitchen ceiling = +5270
 - Reception ceiling = +6100
- Spiral staircase: 14 treads x 201 mm rise = 2814 mm total → meets new doorway at GF FFL.
- Central pole 3300 mm — extends above landing as terminating post / handrail.
- Base-plate fixed to courtyard slab; top fixed to side wall + propped from pole. Final detail by structural engineer.
- The side wall (and the new doorway through it) sits BEHIND the section plane — shown dashed.

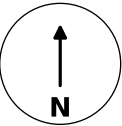

PROJECT	Flat 1, 20 Hornton Street, London W8 4NR	SCALE	1:50 @ A3
DRAWING TITLE	PROPOSED COURTYARD SECTION A-A (showing spiral staircase)	DRAWING NO.	05-B
CLIENT	G. Pearce	DATE	2026-05-25
REVISION	A	SHEET SIZE	A3 (420 x 297)
UNITS	All dimensions in millimetres (mm)	STATUS	FOR PLANNING