

NOTES — REAR COURTYARD PLAN

1. All dimensions in mm at FFL of courtyard slab
(datum FFL −2820 below kitchen ground-floor level).
2. The L-shape comprises:
 - REAR wall (south, 3250 wide) — to rear reception room above; recessed double-door bay at courtyard level (185 cm recess between 72 cm painted cheeks).
 - SIDE wall (east, 3000 long) — to kitchen above; 2 basement-level openings (60 cm bricked-up to reinstate + 123 cm existing glass window).
3. PROPOSED spiral staircase in the inside corner of the L: reclaimed Victorian cast iron, dark painted metal, Ø ≈ 1750 envelope, 14 treads × 201 mm rise.
4. Boundary walls (west + north) retained.
5. External services (downpipe, drainage) to be rationalised — see proposed elevations.
6. Dimensions marked TBC require site re-measure (see dimension_questions.md).


Callouts on plan:

- A


Existing bricked-up opening (600 mm) — REINSTATE as matching basement sash.
- B

Existing basement sash (1230 mm) — retain.
- C

Kitchen window above (ground floor) — PROPOSED enlarge to glazed timber doorway at top of staircase.

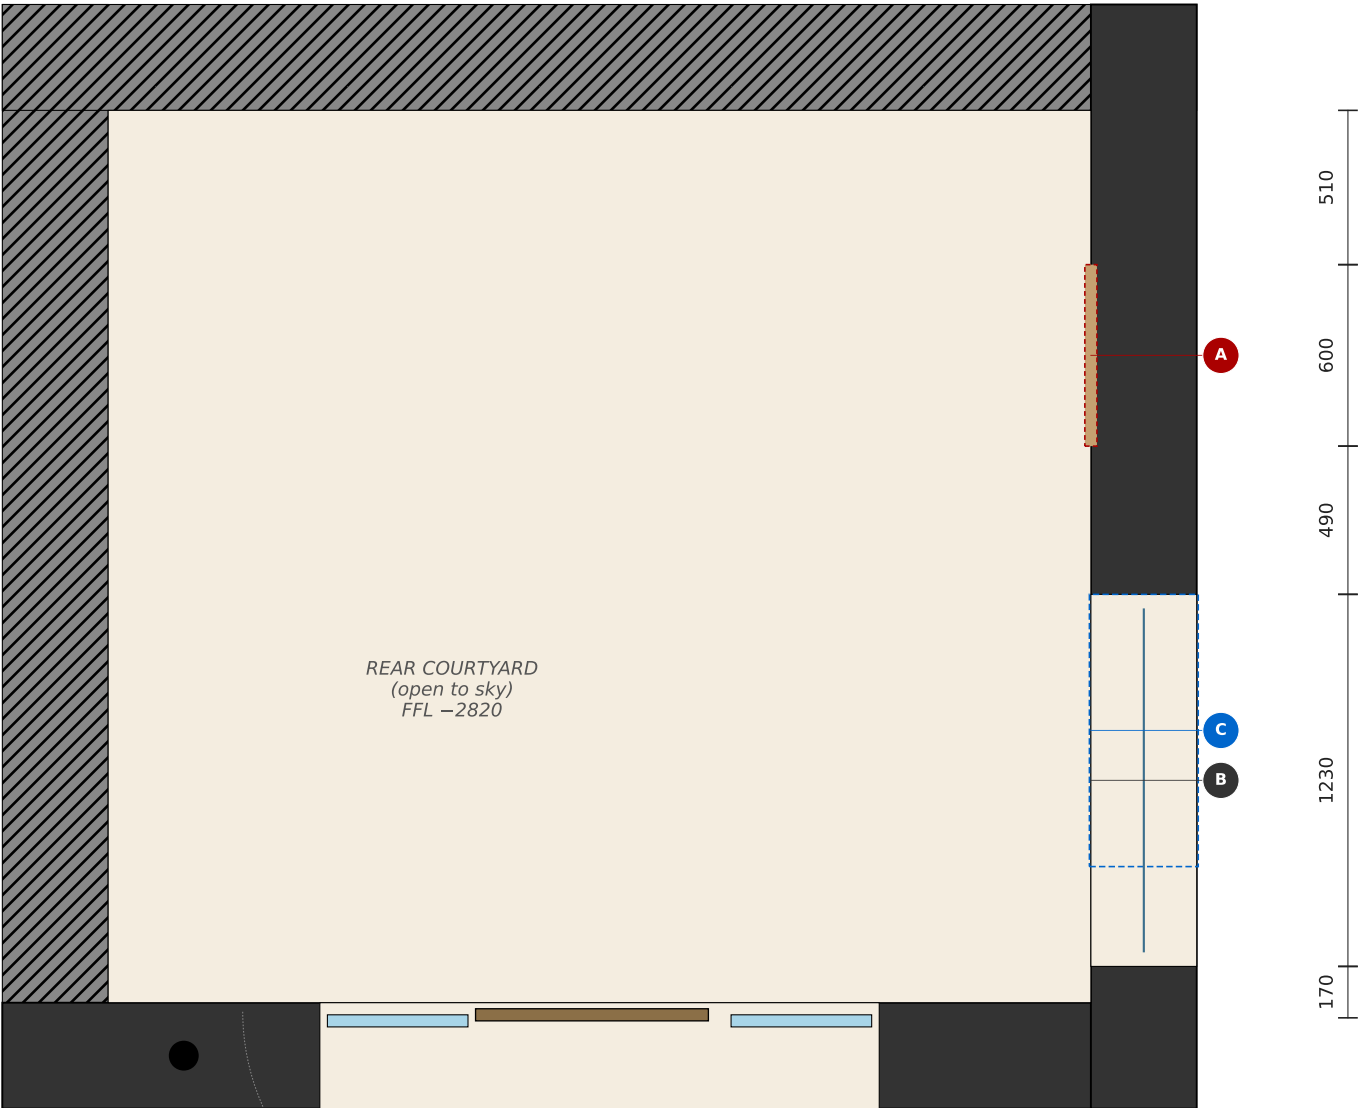

DP
(L corner)

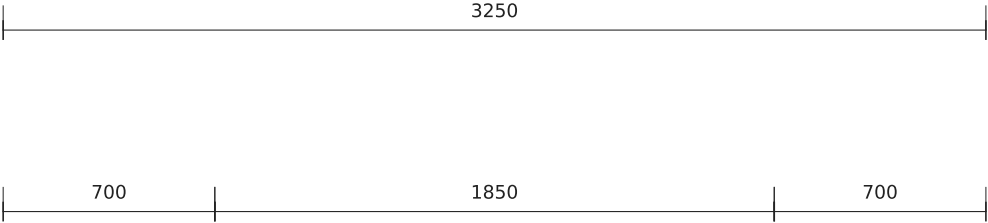

Scale 1:25

PROJECT	Flat 1, 20 Hornton Street, London W8 4NR	SCALE	1:25 @ A3
DRAWING TITLE	EXISTING REAR COURTYARD PLAN	DRAWING NO.	02-A
CLIENT	Grahame McGirr	DATE	2026-05-25
REVISION	B	SHEET SIZE	A3 (420 x 297)
UNITS	All dimensions in millimetres (mm)	STATUS	FOR PLANNING

