


PLAN VIEW
(viewed from above, dwg @ 1:20)

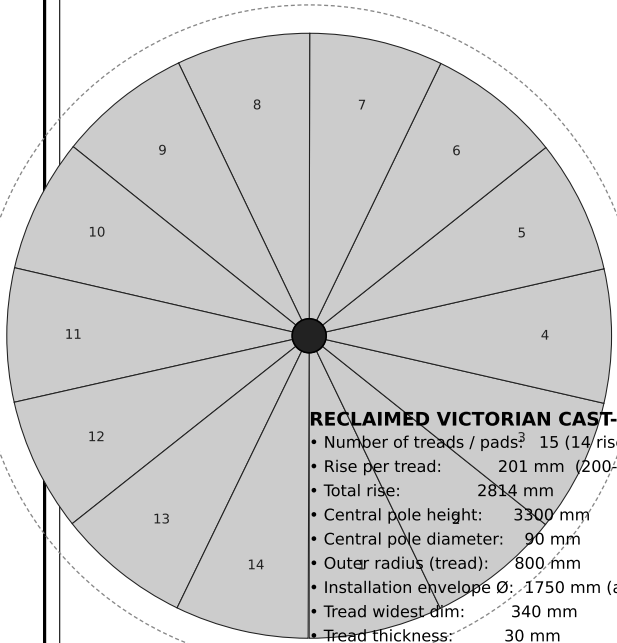

RECLAIMED VICTORIAN CAST-IRON SPIRAL STAIRCASE


- Number of treads / pads: 15 (14 risers + landing pad)
- Rise per tread: 201 mm (200-210 mm verified on artefact)
- Total rise: 2814 mm
- Central pole height: 3300 mm
- Central pole diameter: 90 mm
- Outer radius (tread): 800 mm
- Installation envelope Ø: 1750 mm (allow ~175 cm clear)
- Tread widest dim: 340 mm
- Tread thickness: 30 mm
- UP Rotation per tread: 25.7°
- Handrail height: 900 mm above tread
- Finish: dark painted cast iron / black ironwork

1750 (envelope Ø)

INSTALLATION NOTES

- Base plate bolted to courtyard slab (engineered fixing).
- Top tread / landing pad meets new kitchen-window doorway threshold at +2820 above courtyard slab (= GF FFL).
- Pole top extends to +3300 — terminates above handrail level; cap to be matched to existing handrail Newel detail.
- Side-fixed to side wall via 2 lateral brackets + propped off centre pole.

Final tread detail by engineer; installer to verify achievable rise matches measured site dimension and to fit a small landing pad spacer if dim varies by > ±25 mm.

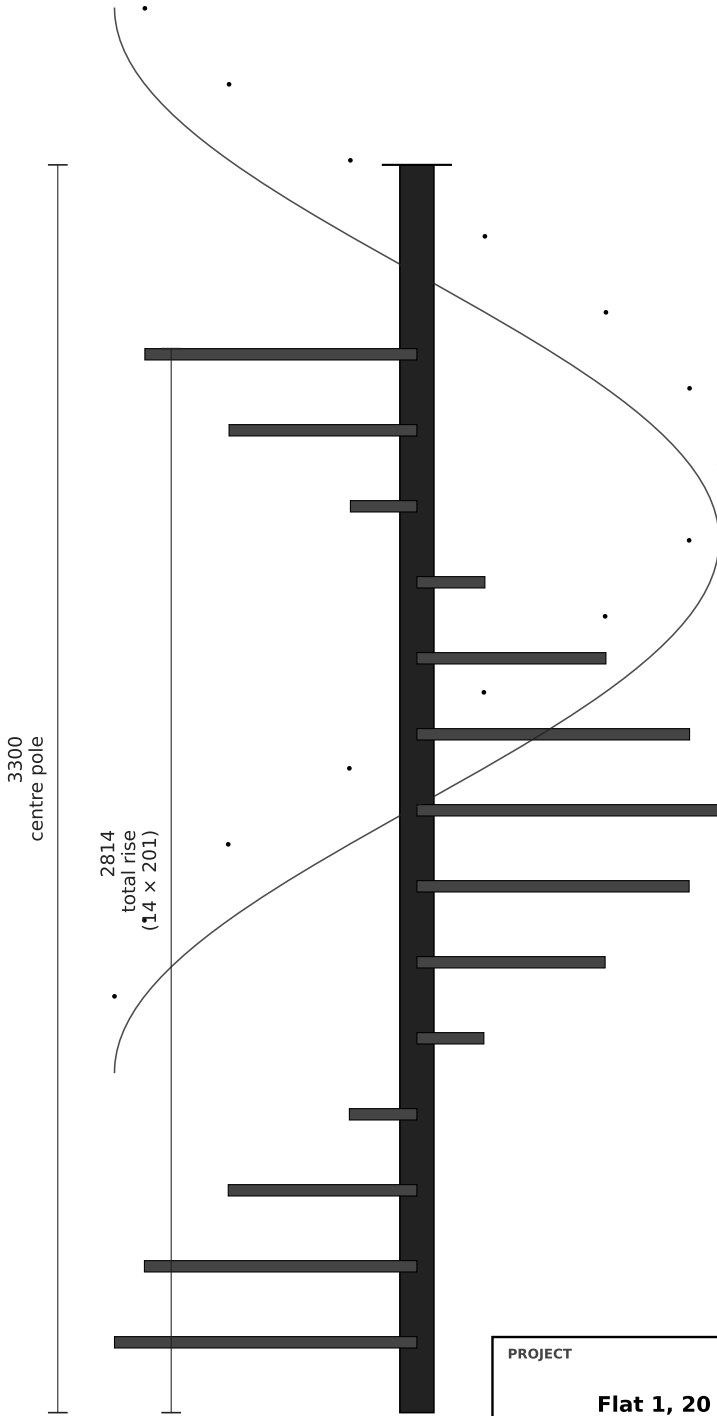

ELEVATION (developed)
Treads laid out side-projected from centre pole

PROJECT	Flat 1, 20 Hornton Street, London W8 4NR	SCALE	1:20 @ A3
DRAWING TITLE	SPIRAL STAIRCASE — Plan & Elevation Detail (1:20)	DRAWING NO.	06
CLIENT	G. Pearce	DATE	2026-05-25
REVISION	A	SHEET SIZE	A3 (420 x 297)
UNITS	All dimensions in millimetres (mm)	STATUS	FOR PLANNING

