

NOTES — REAR COURTYARD PLAN

- All dimensions in mm at FFL of courtyard slab (datum FFL −2820 below kitchen ground-floor level).
- The L-shape comprises:
 - REAR wall (south, 3250 wide) — to rear reception room above; recessed double-door bay at courtyard level (185 cm recess between 72 cm painted cheeks).
 - SIDE wall (east, 3000 long) — to kitchen above; 2 basement-level openings (60 cm bricked-up to reinstate + 123 cm existing glass window).
- PROPOSED spiral staircase in the inside corner of the L: reclaimed Victorian cast iron, dark painted metal, Ø ≈ 1750 envelope, 14 treads × 201 mm rise.
- Boundary walls (west + north) retained.
- External services (downpipe, drainage) to be rationalised — see proposed elevations.
- Dimensions marked TBC require site re-measure (see dimension_questions.md).


Callouts on plan:

- A

Existing bricked-up opening (600 mm) — REINSTATE as matching basement sash.
- B

Existing basement sash (1230 mm) — retain.
- C

Kitchen window above (ground floor) — PROPOSED enlarge to glazed timber doorway at top of staircase.

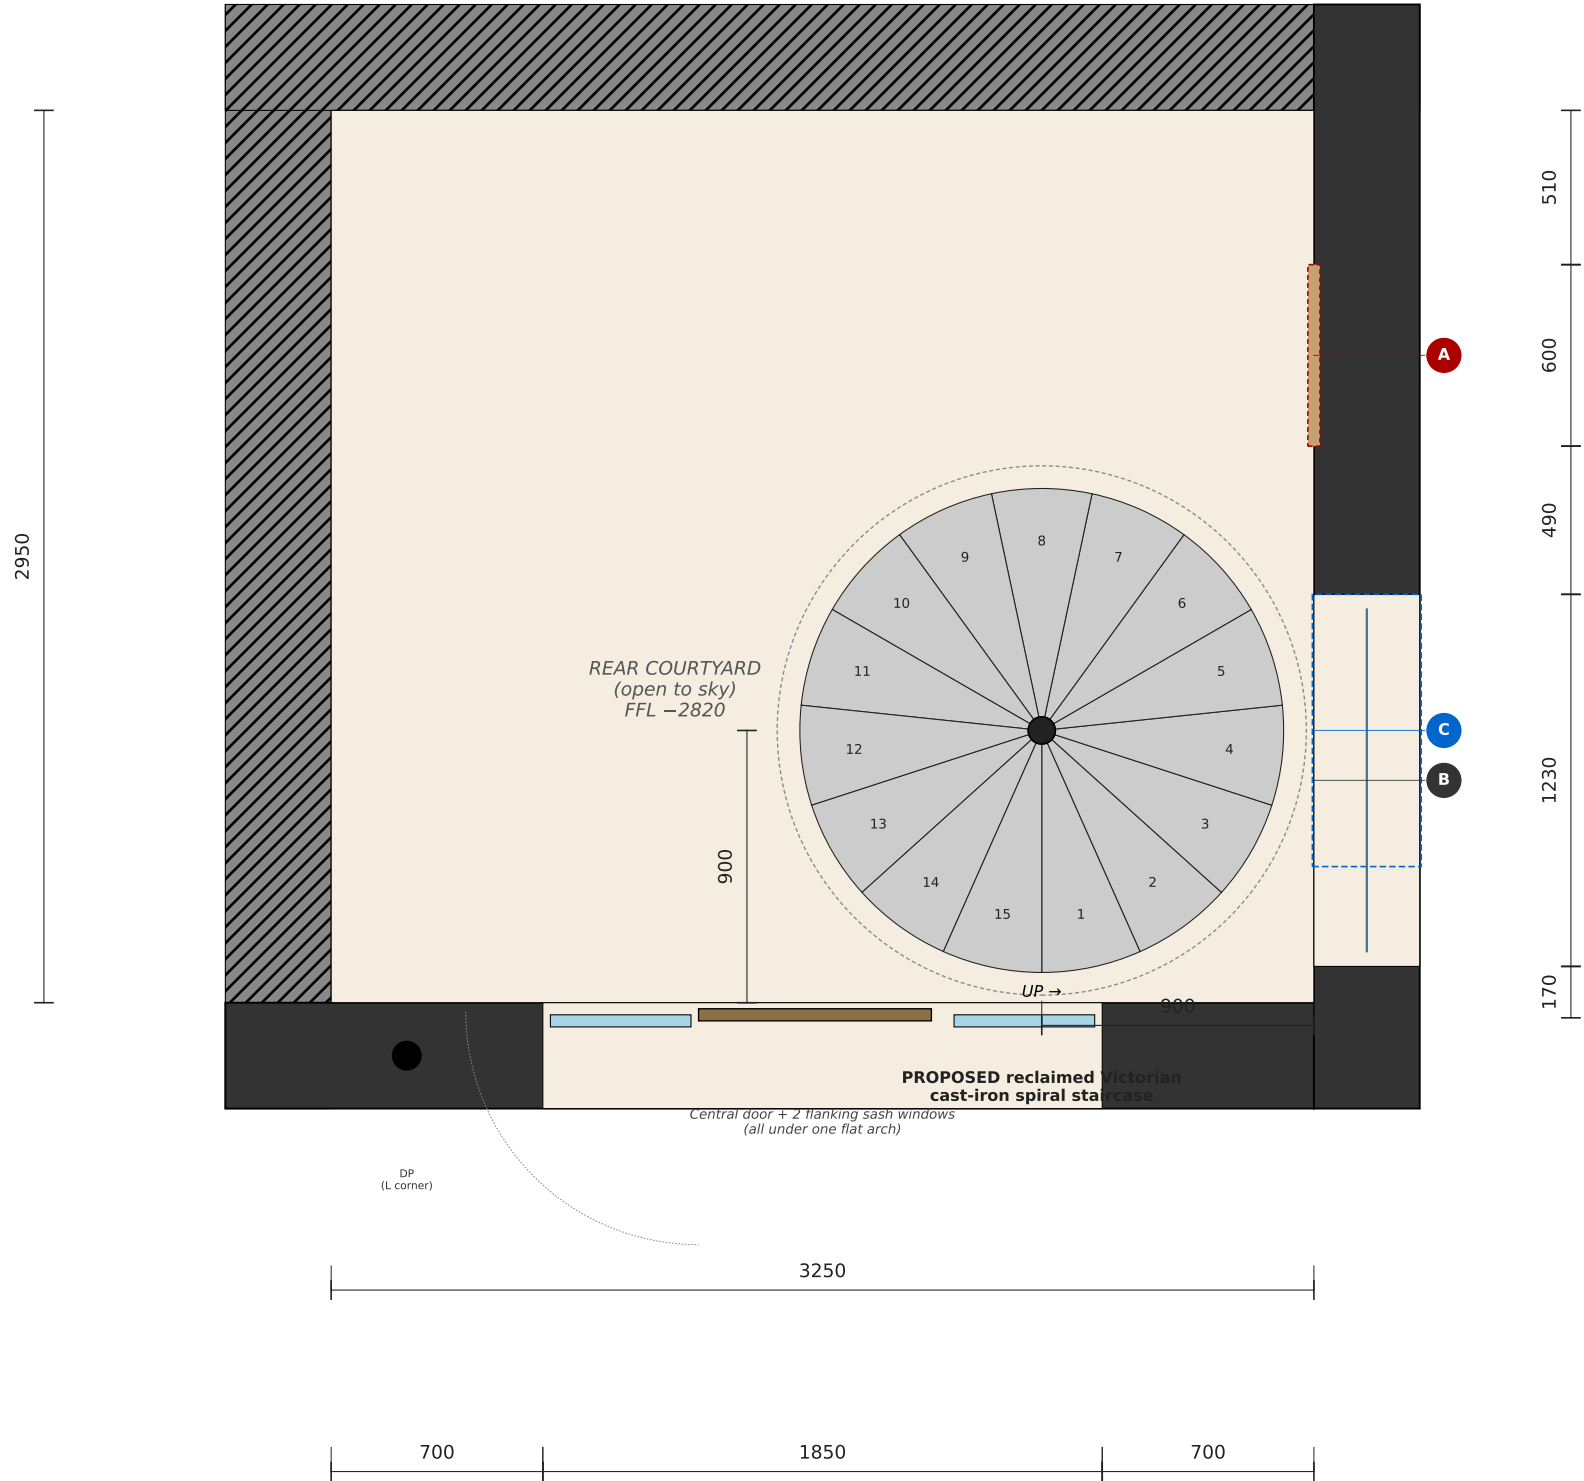

PROJECT	SCALE
Flat 1, 20 Hornton Street, London W8 4NR	1:25 @ A3
DRAWING TITLE	DRAWING NO.
PROPOSED REAR COURTYARD PLAN	02-B
CLIENT	DATE
Grahame McGirr	2026-05-25
REVISION	SHEET SIZE
B	A3 (420 x 297)
UNITS	STATUS
All dimensions in millimetres (mm)	FOR PLANNING

