


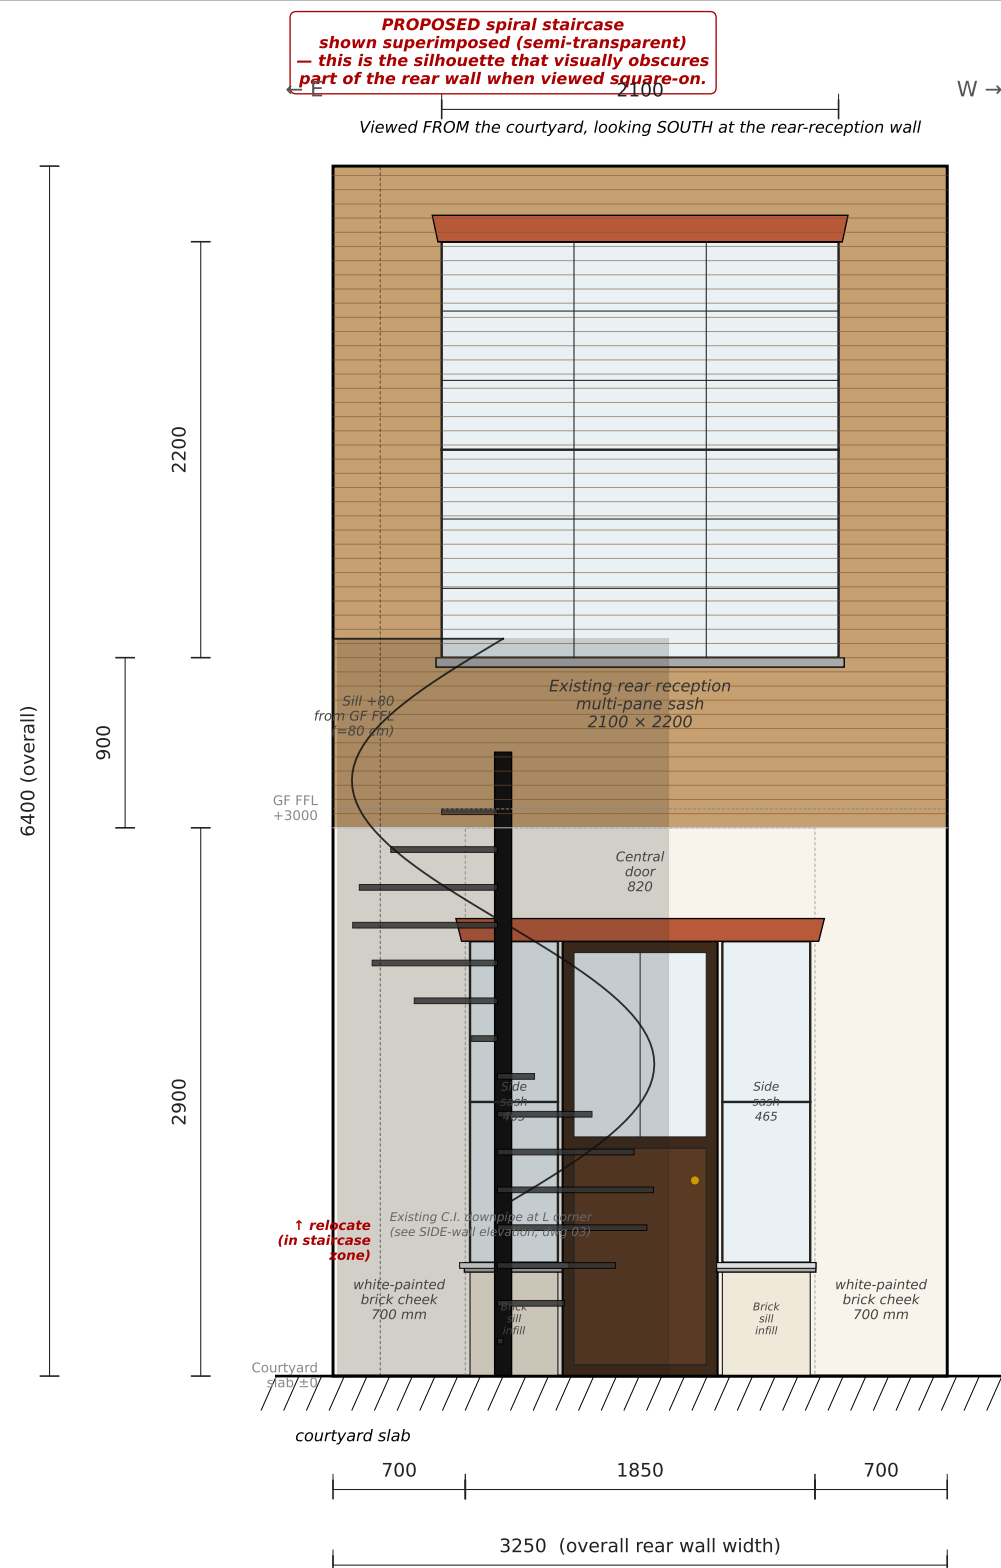

NOTES — REAR WALL ELEVATION

1. View: FROM the courtyard looking SOUTH at the rear wall of the dwelling.
2. The wall is 3250 mm wide (E-W).
3. LOWER (basement) — recessed double-door bay:
 - 700 mm painted-brick cheek (LEFT)
 - 1850 mm recess containing 2 timber leaves
 - 700 mm painted-brick cheek (RIGHT)
 - Recess head at 2900 mm (white-line).
4. UPPER (ground floor) — large multi-pane sash:
 - 2100 mm wide × 2400 mm tall (existing).
 - Sill at 3800 mm above courtyard slab
(= 80 cm above interior GF FFL).
5. Red flat-brick arches over openings (existing).
6. PROPOSED: rear wall is RETAINED AS EXISTING in v1. External services rerouted clear of the new doorway / staircase landing.
7. Re-pointing / make-good where required.

PROJECT	SCALE
Flat 1, 20 Hornton Street, London W8 4NR	1:40 @ A3
DRAWING TITLE	DRAWING NO.
PROPOSED REAR WALL ELEVATION — south wall of courtyard	04-B
CLIENT	DATE
Grahame McGirr	2026-05-25
REVISION	SHEET SIZE
B	A3 (420 x 297)
UNITS	STATUS
All dimensions in millimetres (mm)	FOR PLANNING