


View: NW → SE into the inside corner of the L. Boundary walls (west party + north rear) shown at α≈0.06 so the staircase and openings are visible. Dwelling walls semi-transparent (α≈0.55 upper / 0.92 lower).

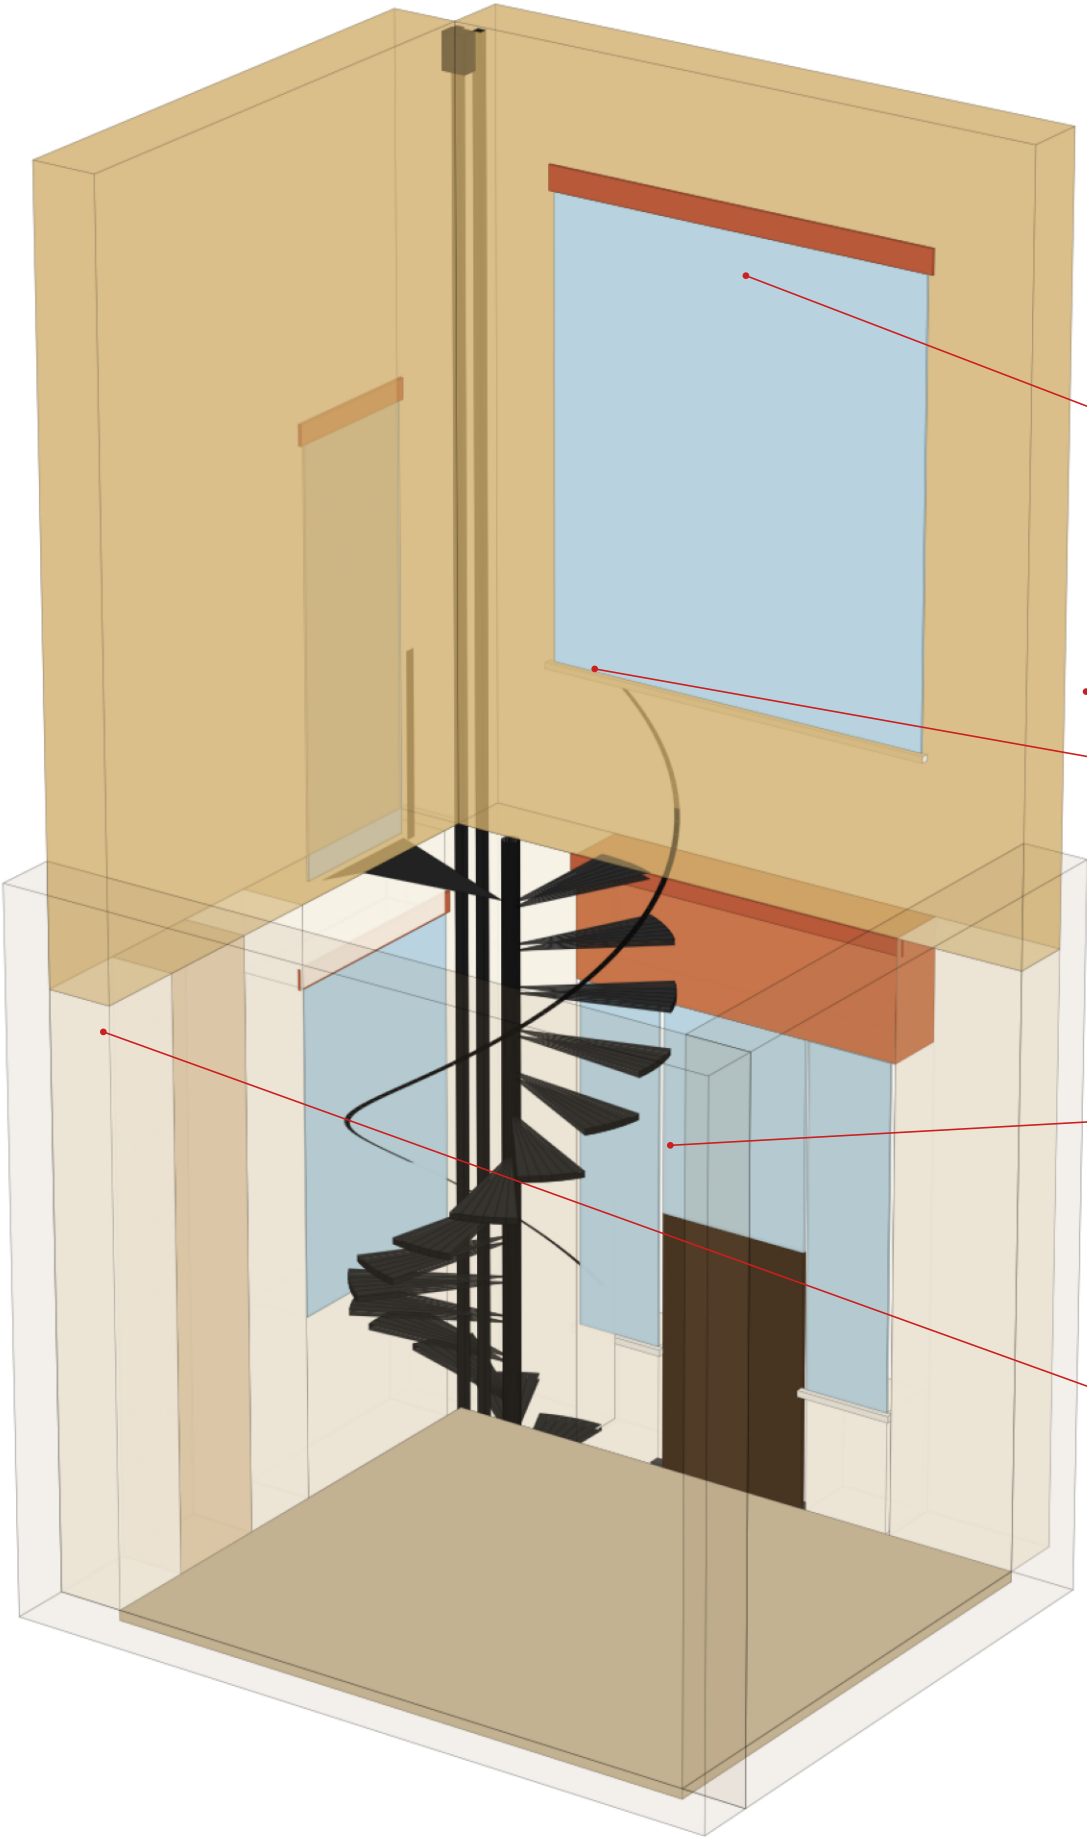

- 1 Kitchen window lowered to floor level and enlarged to form new glazed timber doorway.
- 2 Reclaimed Victorian cast-iron spiral staircase in inside corner of the L (15 risers x 200 mm).
- 3 Existing rear-reception sash (2100 x 2200) retained.
- 4 Red-brick flat arches over openings — retained / matched.
- 5 Existing rear-access bay: central door + 2 flanking sash windows under one arch.
- 6 Existing C.I. downpipe in L corner — rerouted straight down clear of staircase.
- 7 Boundary walls shown in rear courtyard with proposed spiral staircase.

PROJECT	Flat 1, 20 Hornton Street, London W8 4NR	SCALE	1:50 @ A3
DRAWING TITLE	3D AXONOMETRIC REAR COURTYARD WITH PROPOSED SPIRAL STAIRCASE	DRAWING NO.	10
CLIENT	Grahame McGirr	DATE	2026-05-25
REVISION	B	SHEET SIZE	A3 (420 x 297)
UNITS	All dimensions in millimetres (mm)	STATUS	FOR PLANNING

