


NOTES — SIDE WALL ELEVATION

1. View: FROM the courtyard looking EAST at the wall between courtyard and kitchen.
2. The wall is ~3000 mm long (N→S).
3. LOWER (basement) — 2 windows side-by-side:
 - 600 mm bricked-up former opening (LEFT)
 - 1230 mm existing basement sash (RIGHT)
4. UPPER (ground floor) — kitchen window, structural recess ~900 mm, glass gap 660.
5. Datums: courtyard slab = 0; GF FFL +2820; white-painted brick to +2900 (white-line).
6. Existing cast-iron downpipe currently crosses line of proposed new doorway — RATIONALISE.

PROPOSED:

- Reinstate bricked-up opening as basement sash to match adjacent existing window.
- Kitchen window enlarged downward to GF FFL to form glazed timber doorway as top of new spiral-staircase landing.
- Downpipe rerouted south of doorway.
- Match white sash, red flat-arch lintels, yellow-stock brick infill.

Viewed FROM the courtyard, looking EAST at the kitchen-side wall

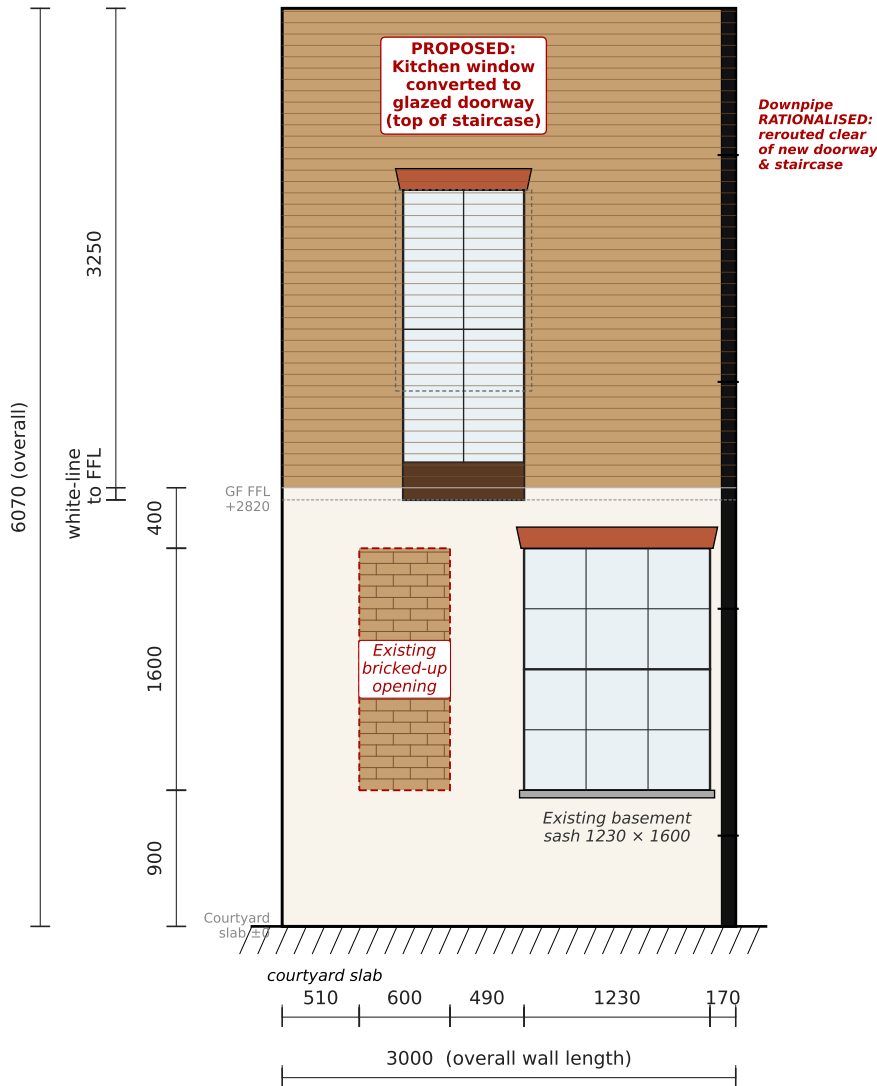

Scale 1:50



PROPOSED SIDE WALL ELEVATION — kitchen-side, east wall of courtyard

PROJECT	Flat 1, 20 Hornton Street, London W8 4NR	SCALE	1:50 @ A3
DRAWING TITLE		DRAWING NO.	03-B
CLIENT	G. Pearce	DATE	2026-05-25
REVISION	A	SHEET SIZE	A3 (420 x 297)
UNITS	All dimensions in millimetres (mm)	STATUS	FOR PLANNING