

Measured Schematic Reconstruction Pack

Before and after floorplans drawn from the estate plan plus hand-drawn proposal sketches

This pack redraws the four requested plans as new vector floorplans, not pasted source images. It uses the printed estate-plan dimensions as the geometric base and overlays the hand-drawn proposed changes. Dimensions are labelled directly on the plans and repeated in the registers. Explicit printed/handwritten dimensions are separated from inferred dimensions.

Important: this is a carefully reasoned reconstruction for AI/design coordination. It is not a construction survey and should not be used for ordering doors, steel, glazing, sanitaryware, or joinery without site verification.

Included floorplans

- 1. Ground floor - existing / before
- 2. Ground floor - proposed / after
- 3. Lower floor / basement - existing / before
- 4. Lower floor / basement - proposed / after
- 5. Consolidated dimension register and unresolved checks

Legend


- Existing/retained walls
- Proposed openings / changes
- Explicit printed or handwritten dimensions
- Inferred / setting-out / uncertain dimensions
- Context, fixtures, stairs, labels

Key corrections used

Ground opening	4.70m = 0.60m nib + 3.40m clear + 0.70m nib
Ground width	4.34m printed existing principal width retained separately
Ground front depth	5.70m from hand sketch 570 and plan scaling
Basement width	5.70m printed existing; 6.10m proposed sketch span flagged
Critical door	1.245m wide x 2.450m high

1. GROUND FLOOR - EXISTING / BEFORE

Higher-fidelity vector trace from estate plan crop. Not an image paste. Dimensions repeated in register.

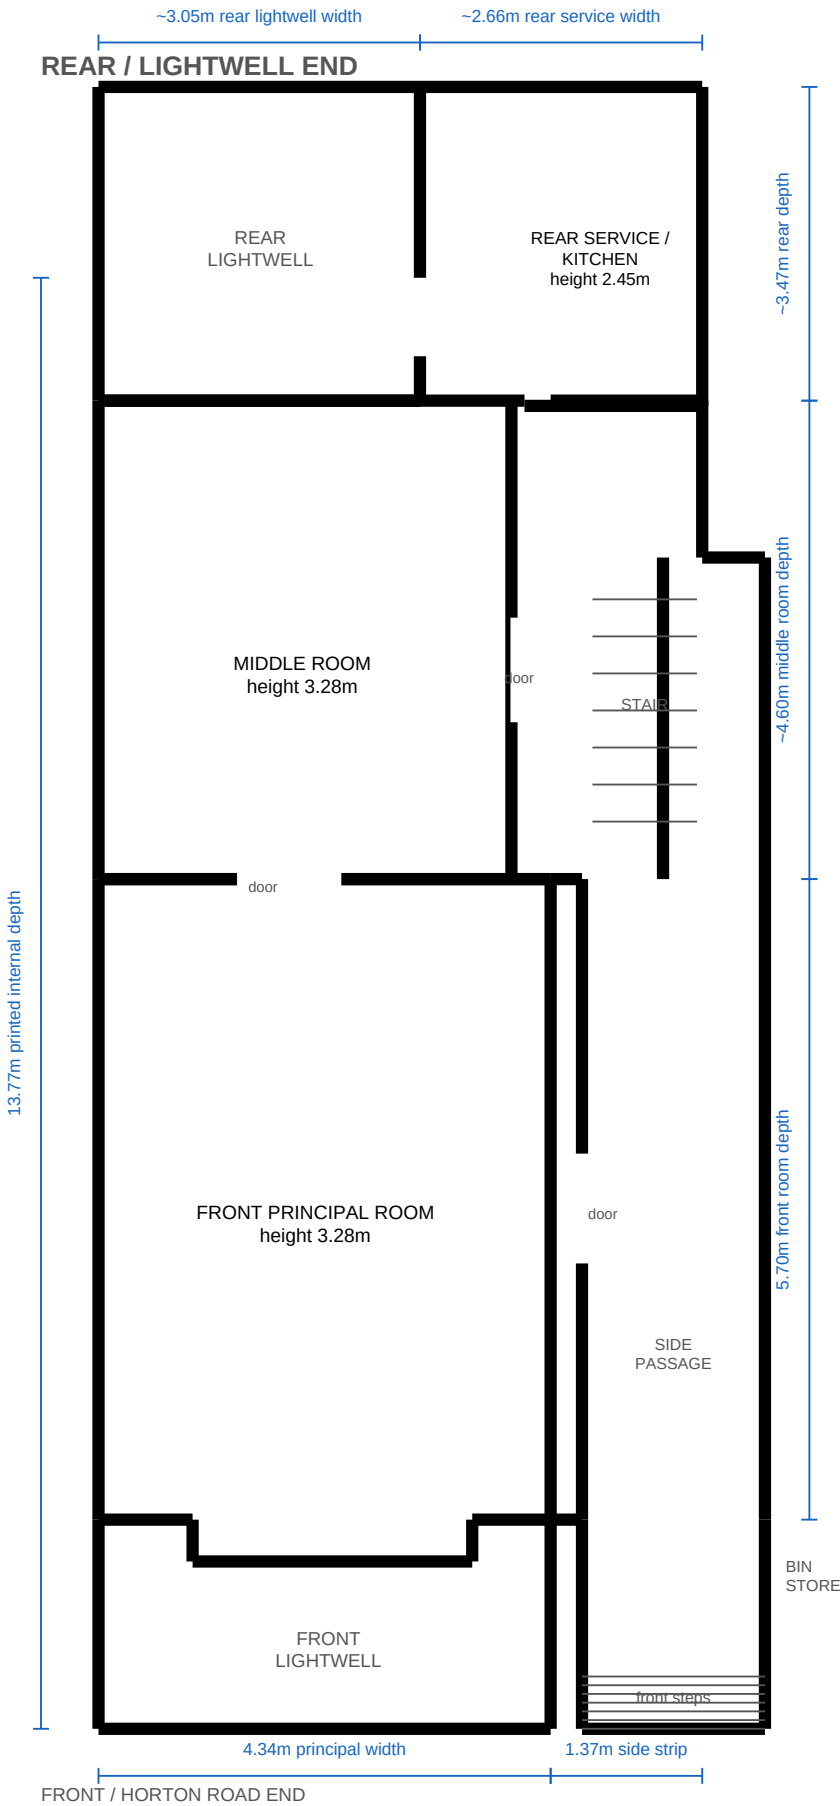


Dimension register - existing ground

Item	Dimension / note
Overall depth	13.77m printed blue dimension through main ground-floor zone.
Principal width	4.34m printed blue dimension across main room.
Side strip	1.37m measured from printed side strip / stair-lightwell zone.
Front room	4.34m x 5.70m. Depth confirmed by hand sketch 570 and scale check.
Middle room	~4.60m deep, inferred from printed plan proportions using 4.34m width.
Rear lightwell	~3.05m x ~3.47m inferred from estate-plan scale.
Rear service/kitchen	~2.66m x ~3.47m inferred; ceiling height printed 2.45m.
Stepped RH zone	Right-side passage, stair stack, front/bin-store zone traced from existing plan.
Heights	3.28m to front/middle rooms; 2.45m to rear service room.
Caution	Inferred dimensions are for schematic coordination only, not ordering.

2. GROUND FLOOR - PROPOSED / AFTER

Vector reconstruction from hand sketch over estate-plan geometry. Red = proposed opening / alteration; blue = explicit dimensions; orange = inferred/setting-out.

REAR / PROPOSED WET + SAUNA END

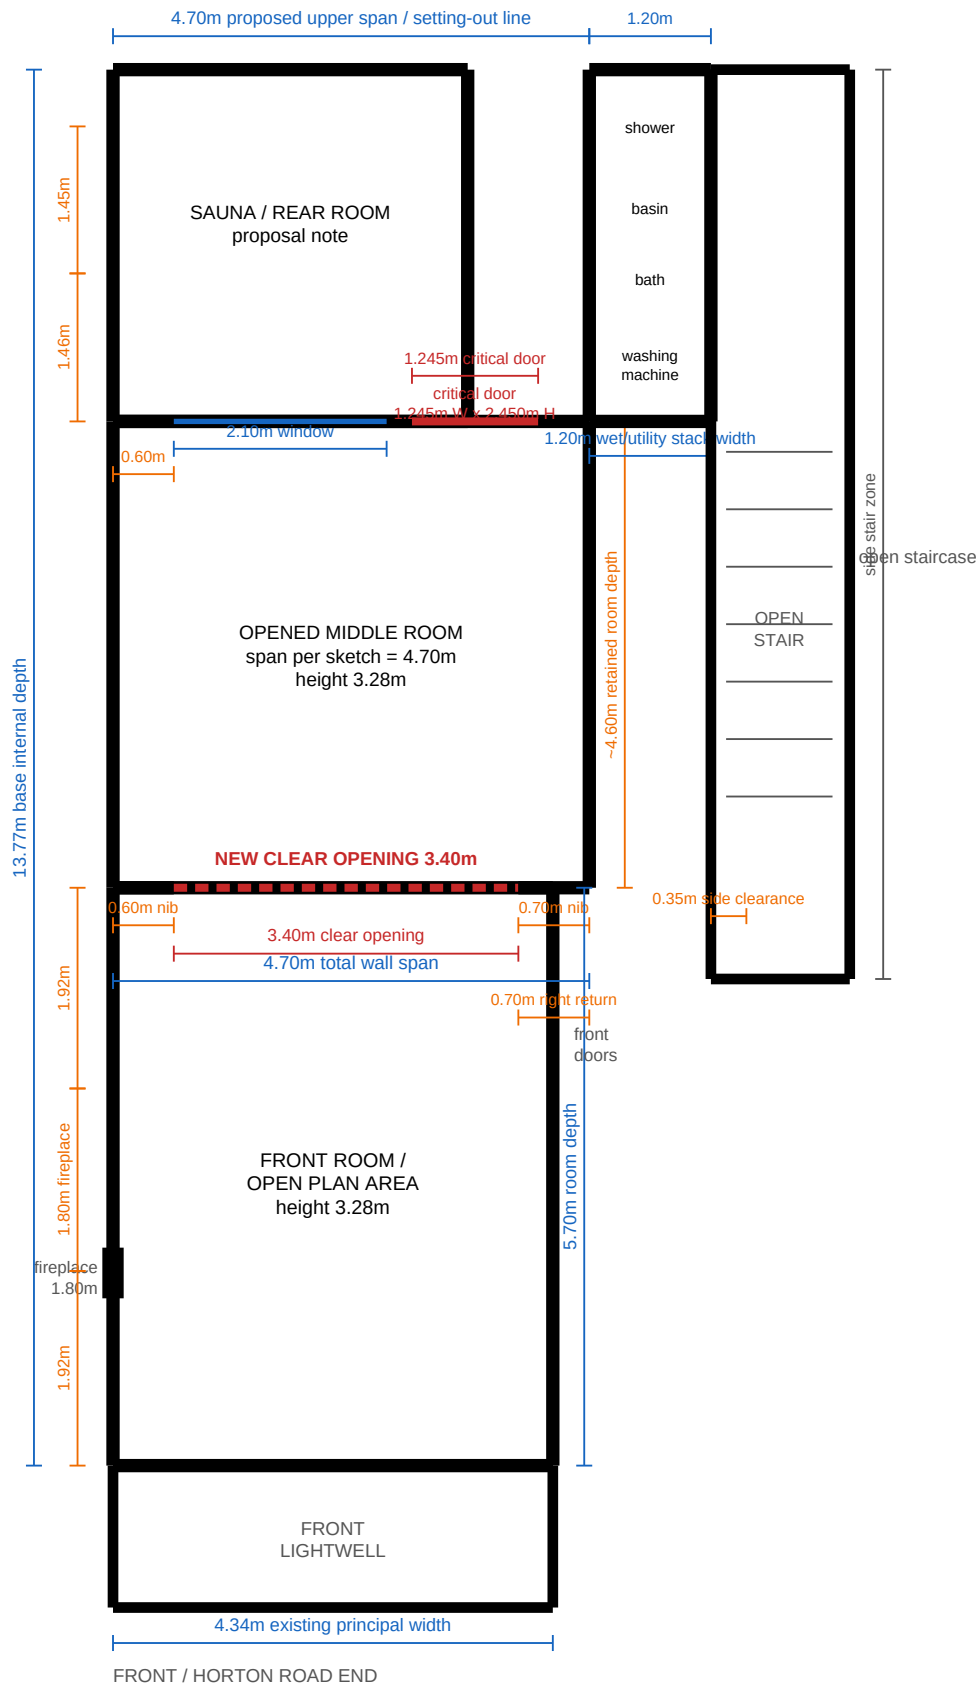


Dimension register - proposed ground

Item	Dimension / note
Proposed opening	4.70m total wall span = 0.60m left nib + 3.40m clear opening + 0.70m right nib. User-confirmed logic.
Front room retained	Existing 4.34m width and 5.70m depth retained as base geometry.
Upper proposed span	4.70m shown as hand-sketch setting-out span; differs from printed 4.34m main width and should be site checked.
Critical door	1.245m width x 2.450m height, from handwriting. Note height also equals printed rear room height 2.45m.
Wet/utility block	1.20m width, containing shower / basin / bath / washing machine stack from sketch.
Window	2.10m window with 0.60m offset noted on sketch.
Side clearance	0.35m noted beside open stair; shown as local clearance/setting-out.
Left vertical notes	1.46m / 1.45m / 1.92m / 1.80m fireplace / 1.92m from handwritten left-side chain. Treated as local setting-out.
Confidence	Opening decomposition is high confidence. Exact upper-wall location vs existing structure remains inferred.

3. LOWER FLOOR / BASEMENT - EXISTING / BEFORE

Higher-fidelity vector trace from estate plan crop. Not an image paste. Dimensions repeated in register.

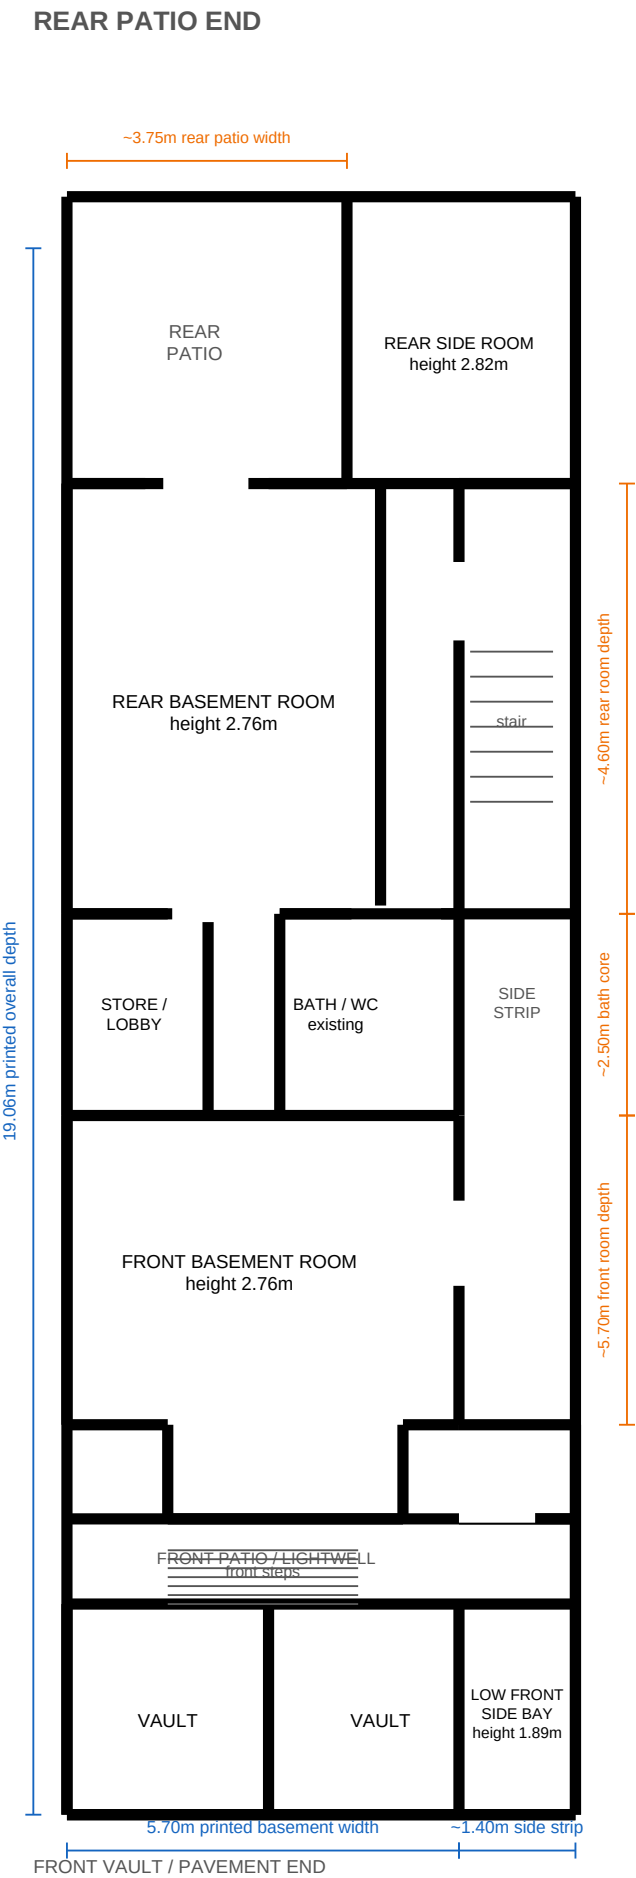


Dimension register - existing basement

Item	Dimension / note
Overall depth	19.06m printed blue dimension.
Main width	5.70m printed blue dimension across principal basement room.
Front room	~5.70m x ~5.70m, depth inferred from plan scale and hand-sketch 570 logic.
Rear room	~5.70m x ~4.60m inferred from estate plan proportions.
Bath/WC core	~5.70m x ~2.50m inferred, located between front and rear rooms.
Rear patio/service	~3.75m rear patio width and rear side room height 2.82m.
Vault/front	Two vaults at front. Sketch later adds 3.13m width and 2.20m depth notes.
Traced detail	Patio, rear room, bath core, front room, vaults, side strip and stair stack drawn as vector trace from estate plan.
Heights	2.76m principal basement rooms, 2.82m rear side room, 1.89m front side bay.
Caution	Detailed compartment dimensions are traced/inferred unless explicitly printed.

4. LOWER FLOOR / BASEMENT - PROPOSED / AFTER

Vector reconstruction from hand sketch. Black = retained/assumed walls; red = new openings; blue = explicit handwritten dimensions; orange = inferred/uncertain setting-out.

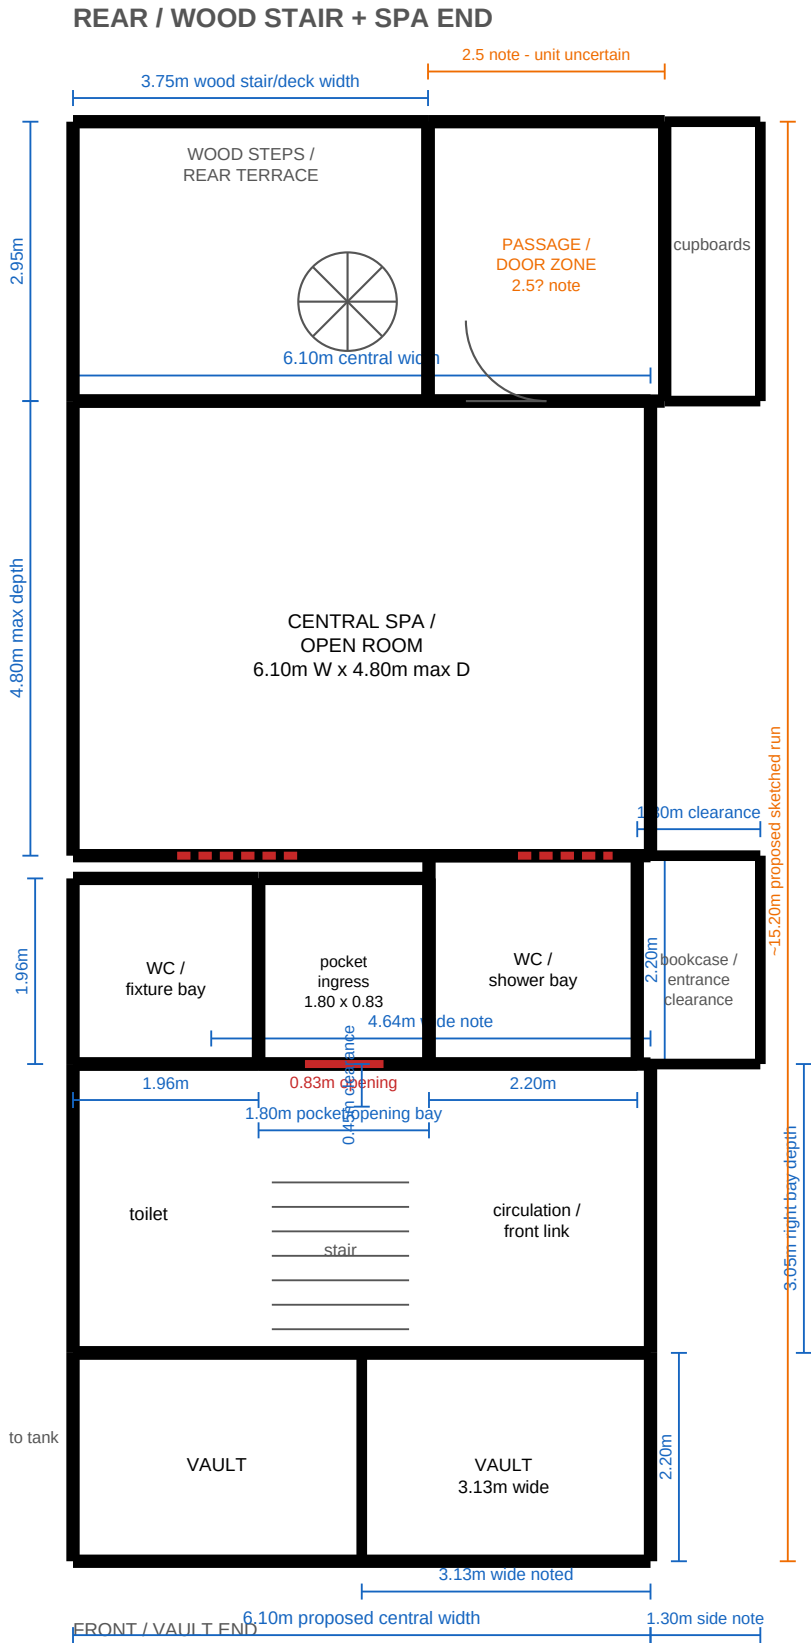

Dimension register - proposed basement

Item	Dimension / note
Rear deck/stair	3.75m x 2.95m handwritten wood stair/deck area.
Central spa room	6.10m width x 4.80m maximum depth. Width exceeds printed 5.70m, so may include side/cupboard/wall thickness allowance.
Left WC bay	1.96m x 1.96m from handwritten 196 / 196.
Pocket/ingress bay	1.80m x 0.83m from handwritten 180 x 83.
Right WC/shower bay	2.20m x 2.20m from handwritten 220 / 220.
Right clearance	1.30m to bookcase/entrance from handwritten 130cm.
Middle clearance	0.45m local clearance/nib from handwritten 45cms.
Lower right/front	4.64m wide note and 3.05m depth note shown in lower circulation/right bay.
Vault	3.13m wide and 2.20m deep noted at vault area.
Uncertain	The top right 2.5 note may be 2.5m or a shorthand. Shown orange, not treated as verified.

5. CONSOLIDATED DIMENSION REGISTER

Machine-friendly summary of every explicit and major inferred dimension used in the four plans.

B-ACT-01	Basement overall depth	19.06m	Printed	High
B-ACT-02	Basement main width	5.70m	Printed	High
B-ACT-03	Basement rear/side height	2.82m	Printed	High
B-ACT-04/05	Basement principal heights	2.76m	Printed	High
B-ACT-06	Basement front side height	1.89m	Printed	High
G-ACT-01	Ground overall internal depth	13.77m	Printed	High
G-ACT-02	Ground principal width	1.34m	Printed	High
G-ACT-03	Horton Road pavement/front offset	2.94m	Printed	High
G-ACT-04	Ground rear service height	2.45m	Printed	High
G-ACT-05/06	Ground principal heights	3.28m	Printed	High
G-TGT-OPEN	New opening wall composition	0.60 + 3.40 + 0.70 = 4.70m	User + sketch	High
G-TGT-02	Ground front room depth	5.70m	Sketch 570	High
G-TGT-04/05	Critical door	1.245m W x 2.450m H	Handwritten	High
G-TGT-06	Wet/utility block width	1.20m	Handwritten	Medium-high
G-TGT-07	Right stair clearance	0.35m	Handwritten	Medium
G-TGT-15	Window length	2.10m	Handwritten	Medium-high
G-TGT-left	Left chain segments	1.46m / 1.45m / 1.92m / 1.80m / 1.92m	Handwritten	Medium
B-TGT-01/02	Rear wood deck / stair zone	1.75m x 2.95m	Handwritten	Medium-high
B-TGT-04/05	Central spa room	6.10m W x 4.80m max D	Handwritten	High var
B-TGT-06/07	Left WC bay	1.96m x 1.96m	Handwritten	Medium
B-TGT-08	Pocket/ingress bay	1.80m x 0.83m	Handwritten	Medium
B-TGT-09/10	Right WC bay	2.20m x 2.20m	Handwritten	Medium
B-TGT-11	Bookcase/entrance clearance	1.30m	Handwritten	Medium
B-TGT-12	Middle lower clearance	0.45m	Handwritten	High
B-TGT-13	Lower right width	1.64m	Handwritten	Medium
B-TGT-14/15	Vault dimensions	3.13m wide / 2.20m deep	Handwritten	High/me
B-TGT-16	Lower right bay depth	1.05m	Handwritten	Medium
B-TGT-03	Top right 2.5 note	2.5? unit uncertain	Handwritten	Low

Unresolved checks before construction

1. Confirm whether proposed ground 4.70m span is structural wall-to-wall, finish-to-finish, or includes wall thickness/side-return.
2. Confirm critical door height: 2450mm may be available rear head height rather than actual leaf height.
3. Basement 6.10m proposed width exceeds printed 5.70m basement width by 0.40m; confirm whether it includes side passage/cupboards/wall thickness.
4. Top-right basement 2.5 note is illegible/ambiguous; do not rely on it without measuring.
5. All small nibs/clearances (0.35/0.45/0.60/0.70/1.30m) need on-site setting-out checks.