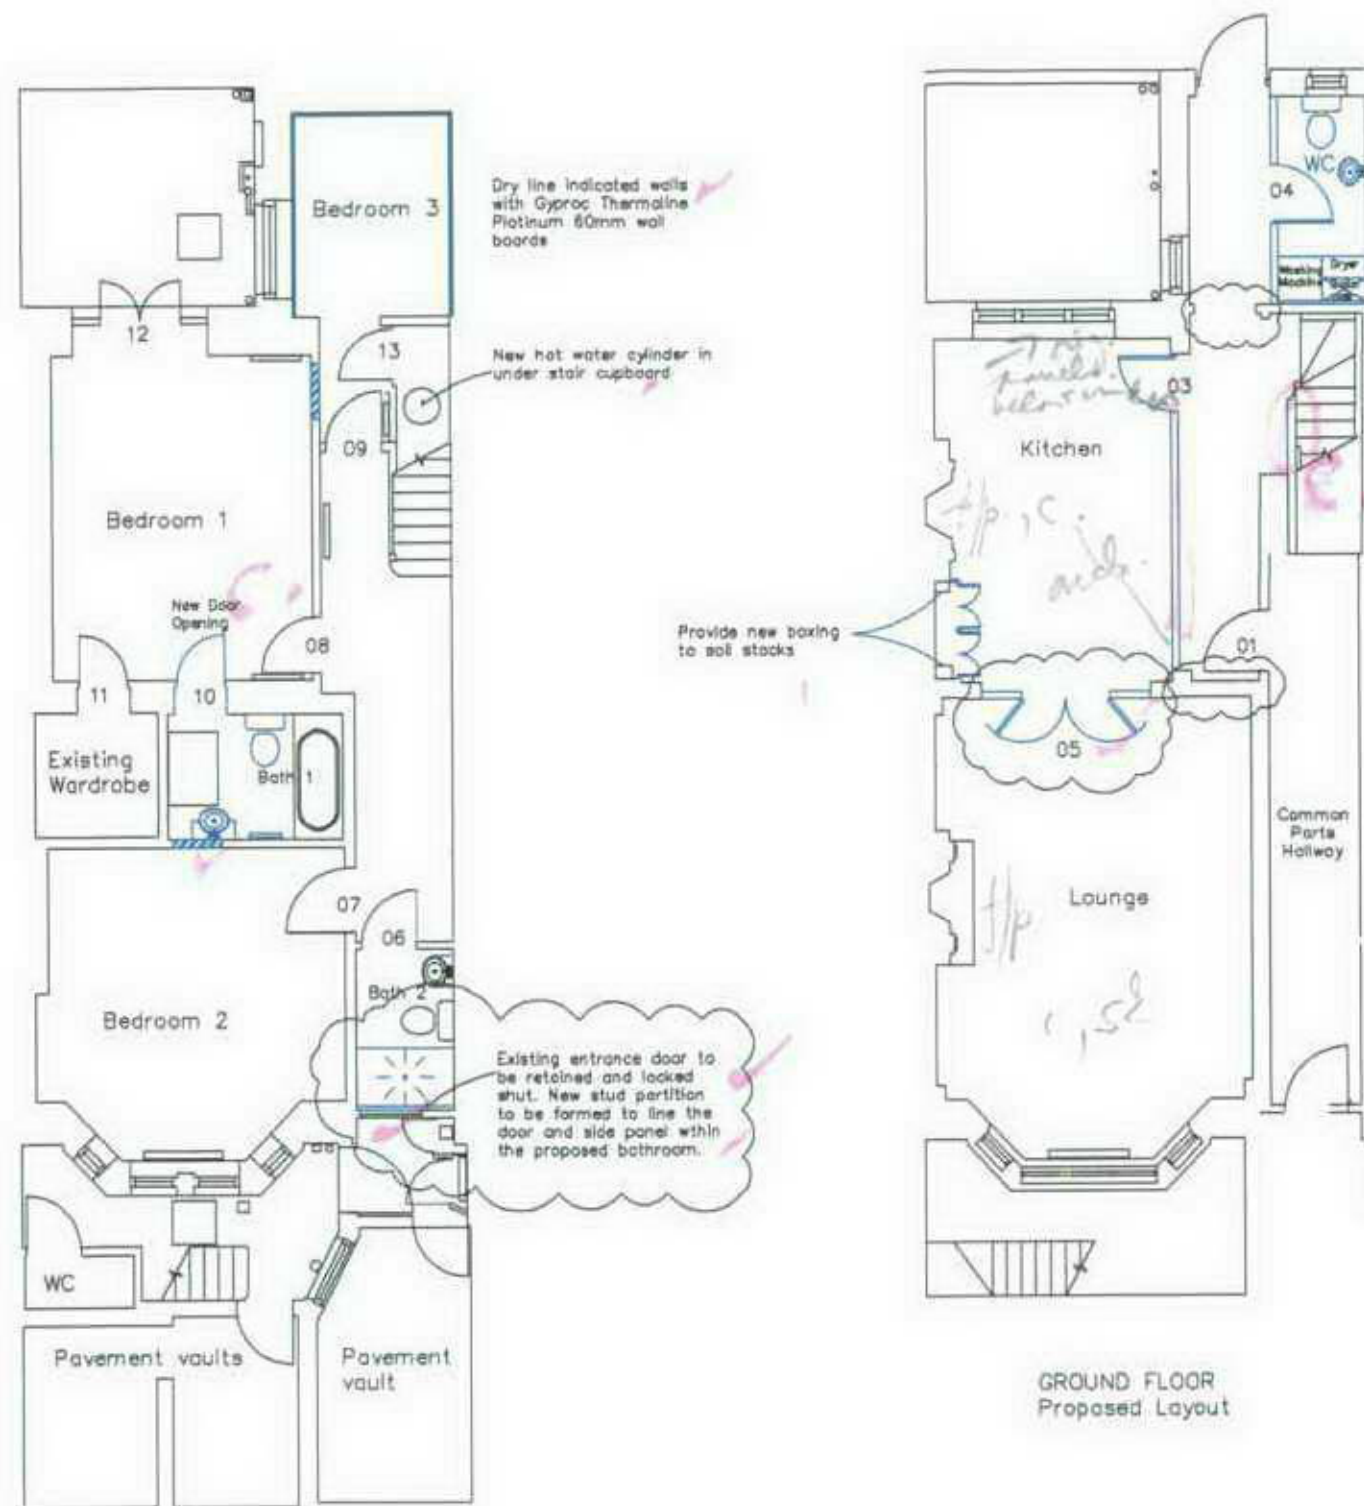


Rev.	Detail	Date
A	Tender issue Door 02 removed, existing kitchen door opening retained, door removed from frame, Door 05 changed to double door, basement entrance door retained, Conservation Officers notes added	25/5/07

REVISED APPROVED DRAWING R.B.K.C. - 6 JUN 2007	
---	--

BUILDING CONSULTANCY 24 HORNTON STREET, KENSINGTON, LONDON W8 5RJ Savills 24 Horton Street, Kensington, London W8 5RJ Tel: +44 (0) 20 7428 8844 Fax: +44 (0) 20 7428 1270 www.savills.co.uk	
--	--

Project 24 HORNTON STREET KENSINGTON, LONDON	
---	--

Drawing PROPOSED LAYOUTS BASEMENT AND GROUND FLOOR	
---	--

Date 01-02-07	Scale 1:100	Sheet A3
Drawn by RH	Checked by	
Drawing No. 45367		
02		A