



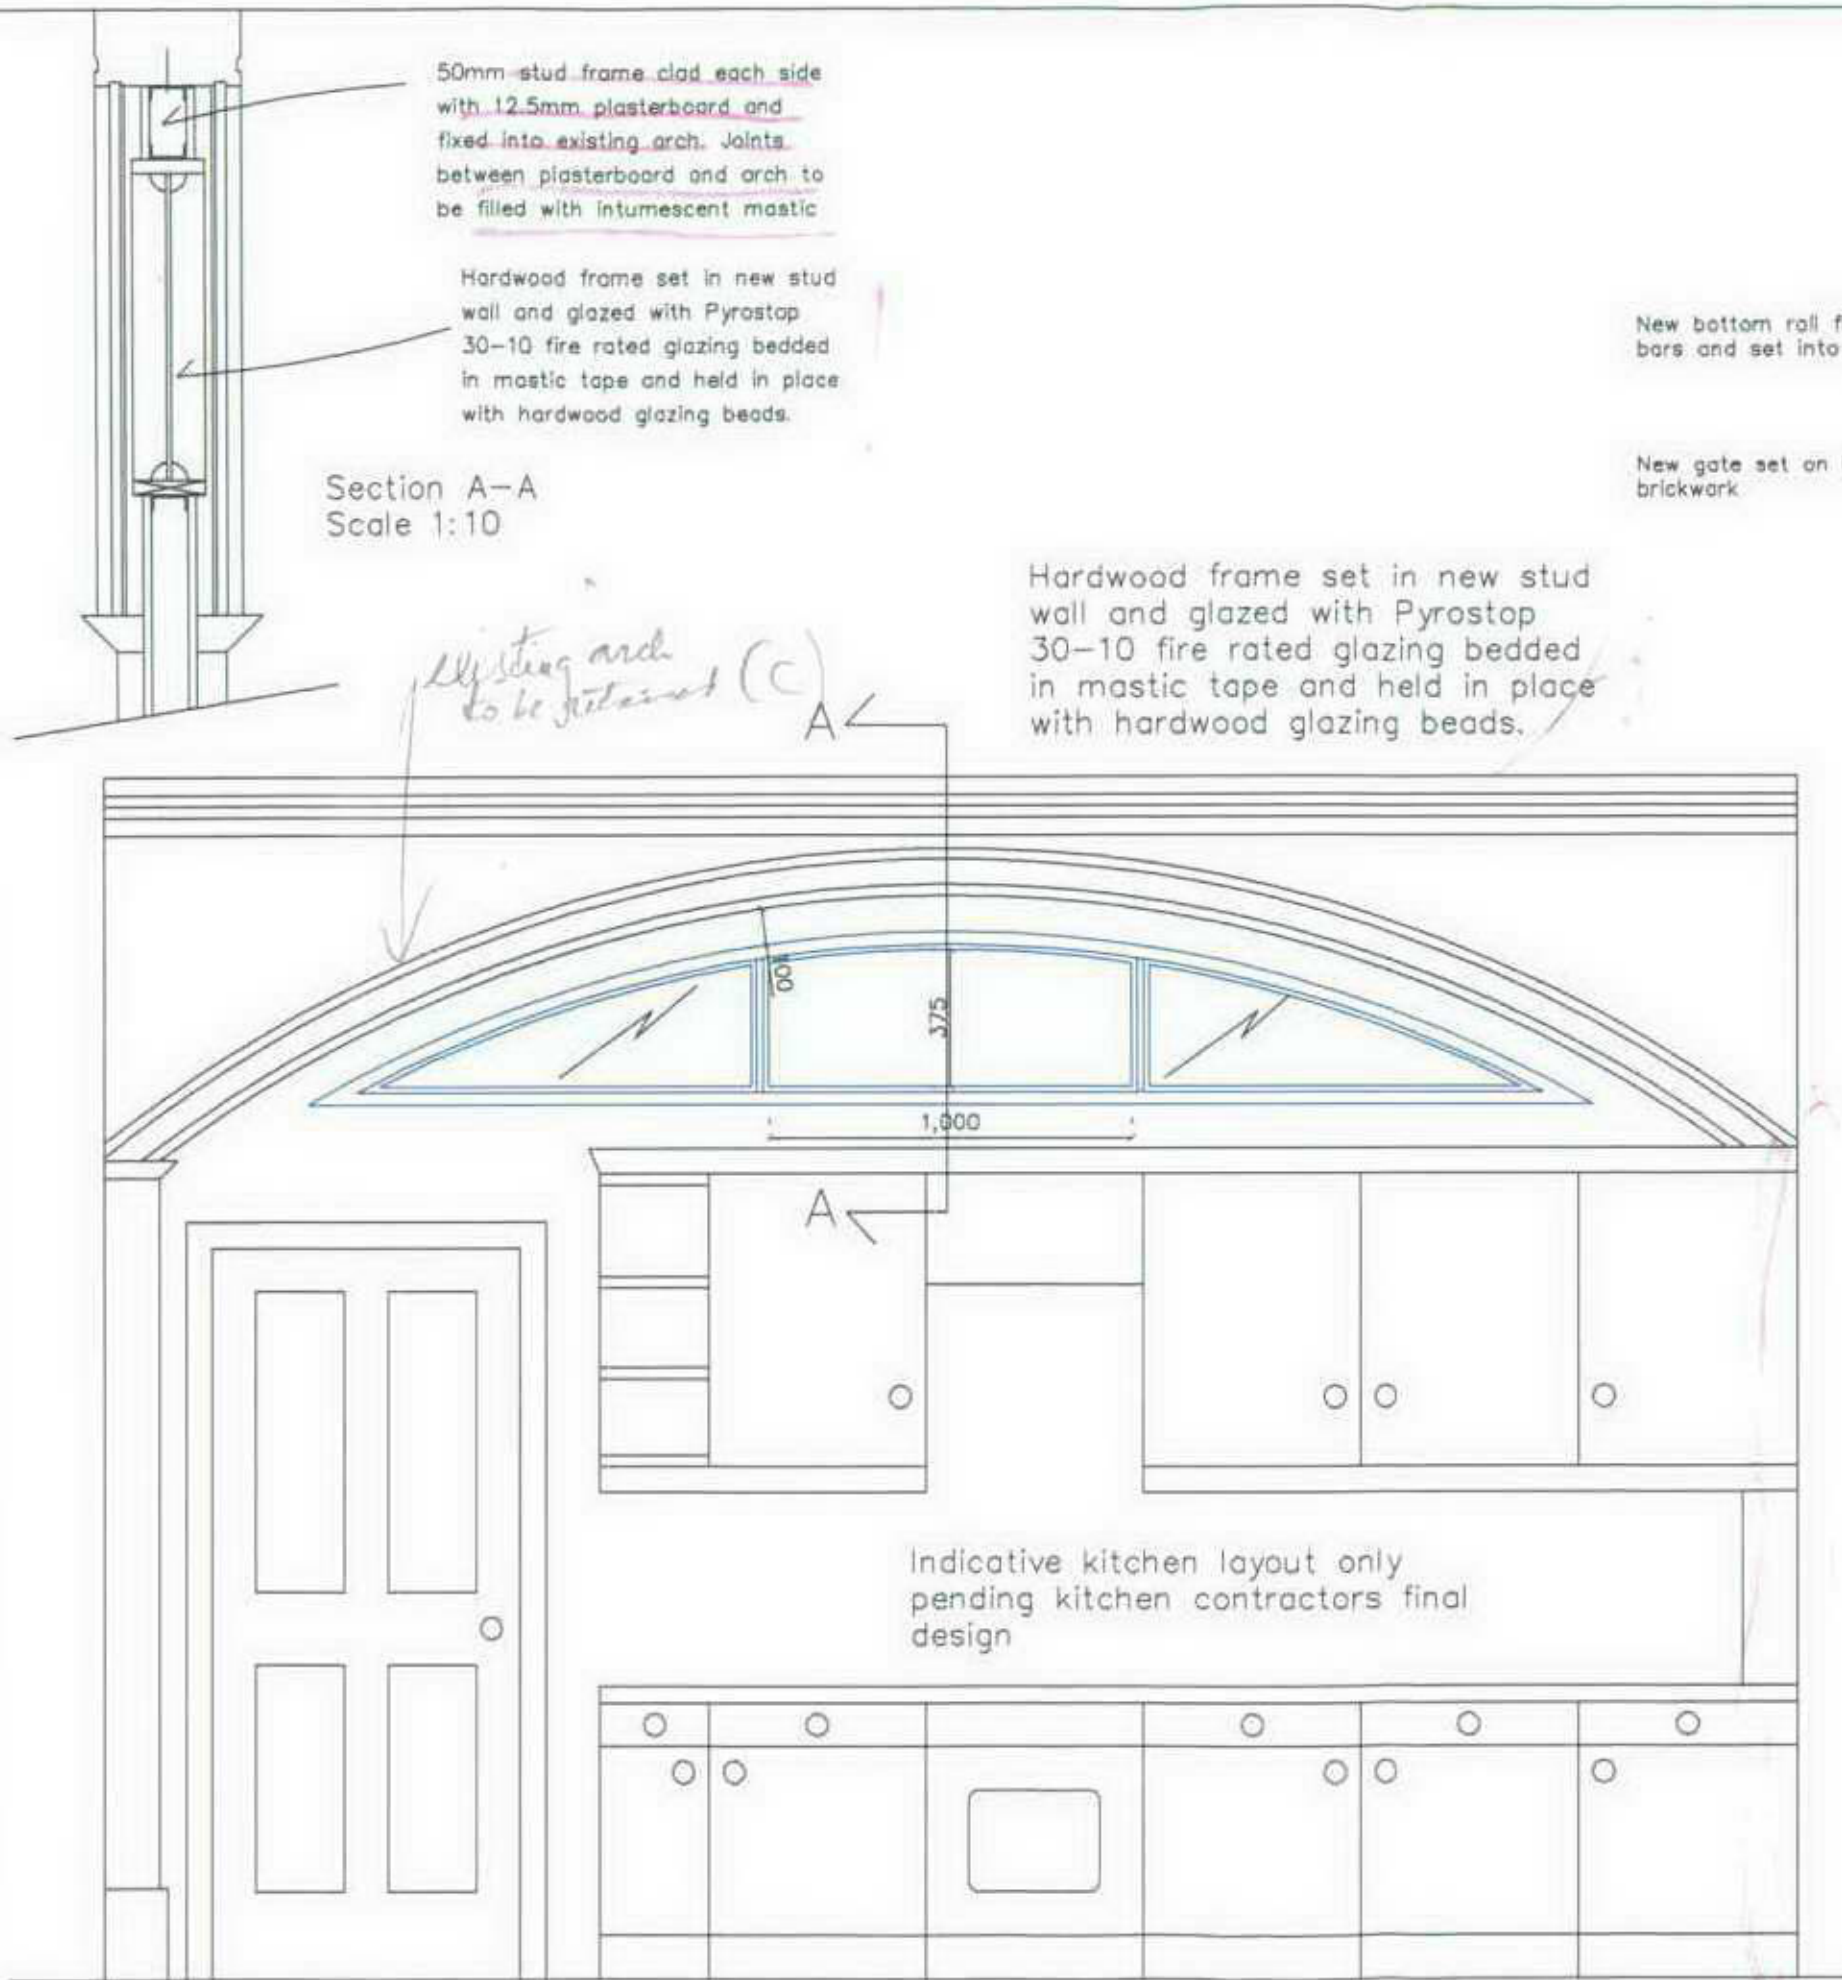

New bottom rail fixed to existing bars and set into brickwork

New gate set on hinges set into brickwork

Lock plate welded to bars and fitted with surface bolt into adjacent wall

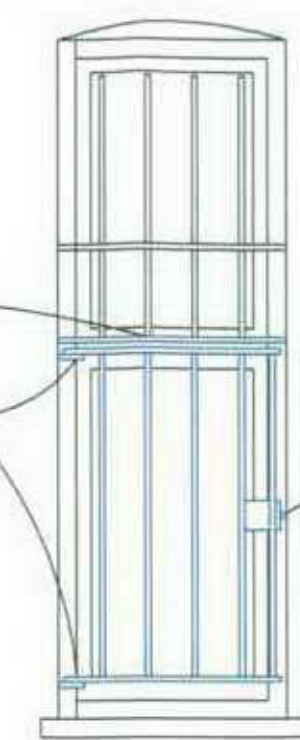

Alterations to Bedroom 2 window bars to provide emergency egress window to basement level

REVISED APPROVED DRAWING
- 6 JUN 2007
K.J.C.

A Section A-A added 25-5-7

REVISIONS



BUILDING CONSULTANCY
DESIGN SERVICES, BUILDING SURVEYING
PROJECT MANAGEMENT, COST CONSULTANCY

Tel +44 (0) 20 7408 8544
Fax +44 (0) 20 7494 1333
www.savills.com

Project
24 HORNTON STREET
LONDON
W8 4NR

Drawing
Proposed Hardwood Screen and alterations to window bars

Date 08/03/07	Scale 1:20	@ A3
Drawn By RH	Checked By	
Drawing No		Rev.
	03	A

