

Application For Listed Building Consent

Description of Works:

Renewal of roof coverings to main roof, damp proofing works to the basement flat and pavement vaults, internal refurbishment of flat 1.

Property Address: 24 Hornton Street,
Kensington,
London W8 4NR

Date: April 2007

LB 70979

Prepared on behalf of

Client: Phillimore 1964 Settlement
c/o Savills (L&P)
8 Bourdon Street,
London,
W1K 3PD

Prepared by

savills

EX	HDC	TP	CAC	AD	CLU	AO
DIR						AK
R.B.	12 APR 2007				PLANNING	
K.C.						
N	C	S		APP	IO	REC
HBS			ARB	FPLN	DES	FEF

25 Finsbury Circus, London EC2M 7EE

CONTENTS

Section 1: Introduction

Section 2: Design Statement

2.1 Renewal of roof coverings to main roof

2.2 Damp Proofing Works to the Basement of the Property

2.3 Damp Proofing Works to the pavement vaults

Section 3: Access Statement

Appendix 1: Listed Building Consent Application Form

Appendix 2: Drawings

Appendix 3: Sketch Proposals and Schedule of Photographs

- 1 **Introduction** 24 Hornton Street is a 6 storey terraced property divided into 4 separate flats to the basement and ground floor, 1st floor, 2nd floor and 3rd and 4th floors respectively.

It is the intention of our client to carry out external redecoration and repair works to the front and rear elevations of the property and the internal refurbishment of flat 1 to the lower and upper ground floor levels during the spring/summer of 2007. A number of these works involve alterations and replacement to the existing fabric of the building and as such an application for listed building consent is required to cover these elements.

A site inspection has been carried out with Helena Benes, Conservation Officer for Kensington and Chelsea London Borough Council, to review the elements of work requiring consent and the following proposals have incorporated her comments accordingly.

2.0 **Design Statement**

In addition to the external redecorations to the building it is intended to renew the existing tile roof coverings to the main mansard roof which are aged and showing signs of deterioration with evidence of repairs undertaken to the tiles and lead-work in the past.

Rising damp has been uncovered to a number of the basement level walls where it is causing damage to the wall finishes. There is also a high level of water ingress to the 3 vaults under the pavement to the front of the building which has resulted in substantial corrosion of the structural steel beams supporting the pavement structure above. It is therefore proposed to repair the steel beams and carry out damp proofing works to the vaults and affected basement level walls while flat 1 is currently vacant.

2.1 Renewal of roof coverings to main roof

The existing roof to the building is a mansard roof with clay tile coverings to the front and rear elevations and asphalt coverings to the flat central section of the roof. The roof structure forms the upper floor level of flat 4 and there are no loft spaces within the mansard structure.

The 3rd and 4th floor windows are timber dormer windows set in the side of the mansard roof. The bonnets to the dormers are covered with lead sheeting.

The tile coverings and lead sheeting are aged and showing signs of wear with patches of replaced tiles and additional slipped tiles requiring further repair.

Our proposals are therefore to replace all leadwork and tile coverings to the main roof.

The lead flashings and dormer coverings will all be replaced on a like for like basis.

The existing tile will be stripped and replaced with new Redland Plain tiles from the Rosemary Classic range, type 81 Light Mixed Brindle Smooth.

Roof Insulation

The exact structure of the roof will not be established until the roof coverings are removed. On similar properties in the area these mansards have been constructed with solid concrete clinker infill between the structural elements which means there is no void within the roof structure to introduce any insulation.

We do not consider the installation of insulation above the infill material to be feasible either as this would raise the level of the roof coverings at ridge levels and bring the plane of the tiles out around the dormer windows at sill and cheek level.

Our proposals are therefore to leave the vertical planes of the roof un-insulated.

2.2 Damp proofing works to the basement of the property

Flat 1 is currently vacant and occupies the lower and upper ground floor level. Rising damp to a number of the basement level walls is causing damage to the wall finishes. It is therefore proposed to carry out damp proofing works to localised areas during the proposed refurbishment works.

The proposals are to strip all wall linings and wall plaster up to 1.1m above floor level to the affected areas, inject a chemical damp course to all walls and re-instate the wall finishes on completion.

All existing skirtings to be stripped will be set aside and re-used where possible, otherwise new skirtings matching the existing profiles will be used. The walls will be rendered at low level with a sand and cement screed and plaster skimmed over to provide a surface ready for redecoration.

2.3 Damp proofing works to the pavement vaults

The proposals are to repair the corroded steel beams supporting the vault roofs and then providing a cement screed to the ceilings, walls and floors to tank the vaults and prevent further ingress of water from the pavement above and the retaining walls to the sides and rear of the vaults.

3.0 Access Statement

The existing flat is currently accessed via steps up from street level into the common parts hallway. Internal access is via a staircase between floors and as such there is no current disabled access to the building.

No alterations are being made to the access arrangements to or around flat 1. As there is no current disabled access we only envisage this building being used by able bodied people.

Appendix 1: Listed Building Consent Application Form

THE ROYAL BOROUGH OF KENSINGTON AND CHELSEA
PLANNING (LISTED BUILDINGS & CONSERVATION AREAS) ACT, 1990
APPLICATION FOR LISTED BUILDING CONSENT / CONSERVATION AREA CONSENT

1. **APPLICANT**
 Name *PHILLIMORE 1464 SETTLEMENT*
F.A.O ROWLAND BULL
 Address *% SAVILLS LLP*
8 BOURDON STREET
LONDON W1K 3PD
 Telephone *020 7016 3736*
- AGENT**
 Name *SAVILLS COMMERCIAL LTD*
F.A.O JAMES FOTHERSTON
 Address *25 FINSBURY CIRCUS*
LONDON
EC2M 7BB
 Telephone *020 7877 4533*
-
2. Full address or location of the land to which this application relates *24 HOLTON STREET*
LONDON
W8 4NR
-
3. Brief particulars of the proposed works *INTERNAL REFURBISHMENT OF FLAT 1*
AND REPLACEMENT OF MAIN ROOF
COVERINGS
-
4. State whether the proposal involves (delete the items which do not apply)
~~(a) Demolition of the building(s)~~
~~(b) Alterations and/or extensions~~
 (c) Other
-
5. State the purpose for which the land is
 (a) now used, or (a) *RESIDENTIAL FLATS*
 (b) if vacant, the last known use (b)
 (c) proposed to be used (c) *RESIDENTIAL FLATS*
-
6. List drawings and plans submitted with the application
01 EXISTING LAYOUTS
02 PROPOSED LAYOUTS
04 ROOF PLAN AND LOCATION PLAN
05 DAWN PHOTOGRAPHS TO THE BASEMENT
-
7. State suitable location on building or within curtilage of building for display of statutory notice in respect of this application *ON RAILINGS TO THE FRONT*
ELEVATION

I / We hereby apply for consent to carry out the works described in this application and on the attached plans and drawings.

Signed

R. Lyle

On behalf of *SAVILLS COMMERCIAL*

Date *10-4-07*

AN APPROPRIATE CERTIFICATE MUST ACCOMPANY THIS APPLICATION (See Notes for Applicants)

Certificate A: Where all the land/building is owned by the applicant.

Certificate B: Where some or all of the land/building is not owned by the applicant but the name/address of the owner(s) is known.

Certificate C: Where some or all of the land is not owned by the applicant and where the ownership of only part of it is known.

Certificate D: Where some or all of the land is not owned by the applicant and the applicant has not been able to find out who owns it.

Freeholder or leaseholder with more than 7 years to run. Certificate A & B can be found overleaf. Certificate C & D are available on request from the Planning Information Office on 0207 361 3012.

You are advised that the Council scans all planning applications and makes them available on the Internet. If this is of concern, please advise us in writing when you submit your application.

**THE ROYAL BOROUGH OF KENSINGTON & CHELSEA
PLANNING (LISTED BUILDINGS & CONSERVATION AREAS) ACT, 1990
CERTIFICATE UNDER SECTION 11, PART 1 OF THE PLANNING (LISTED BUILDINGS &
CONSERVATION AREAS) ACT, 1990**

Complete only one certificate, either A, B, C or D to accompany your application
(see notes for applicants)

CERTIFICATE A

I certify that:

- No person other than the applicant was an owner (a) of any part of the land to which the application relates at the beginning of the period 21 days before the date of this application.
- None of the land to which this application relates constitutes or forms part of an agricultural holding.

Signed: 

On behalf of: *Spirel Conain* Date: *10-11-7*

CERTIFICATE B

I certify that:

- I have/The applicant has given requisite notice to the persons specified below, being persons who on the day 21 days before the date of the application were owners (a) of any part of the land to which the application relates.
- None of the land to which the application relates constitutes or forms part of an agricultural holding.


Owner's name	Address at which notice was served	Date on which notice was served
--------------	------------------------------------	---------------------------------

Signed:


On behalf of:

Date:


Appendix 2: Drawings

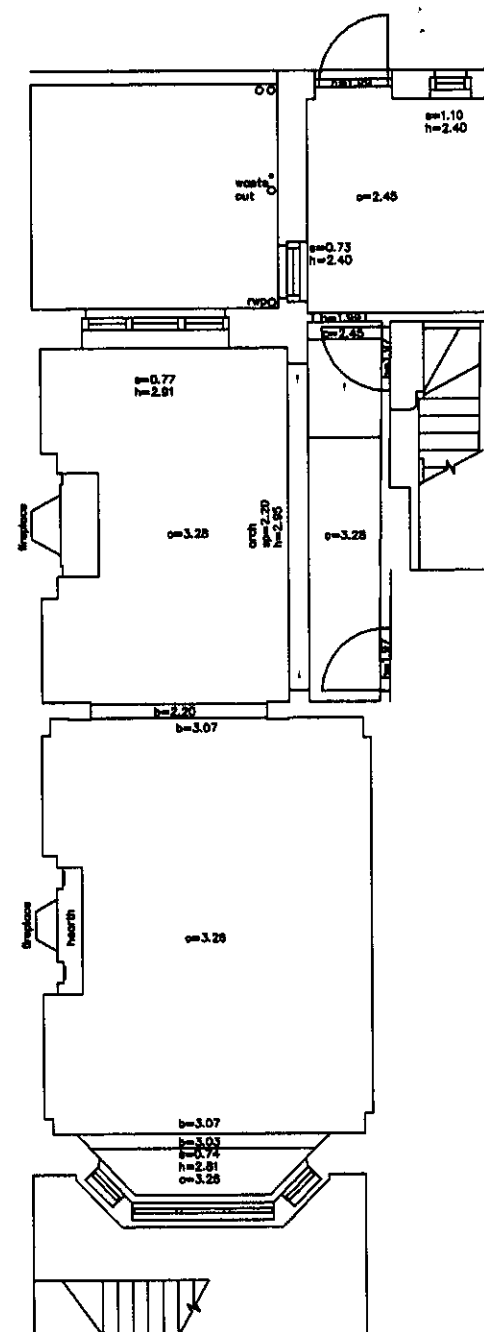

GROUND FLOOR

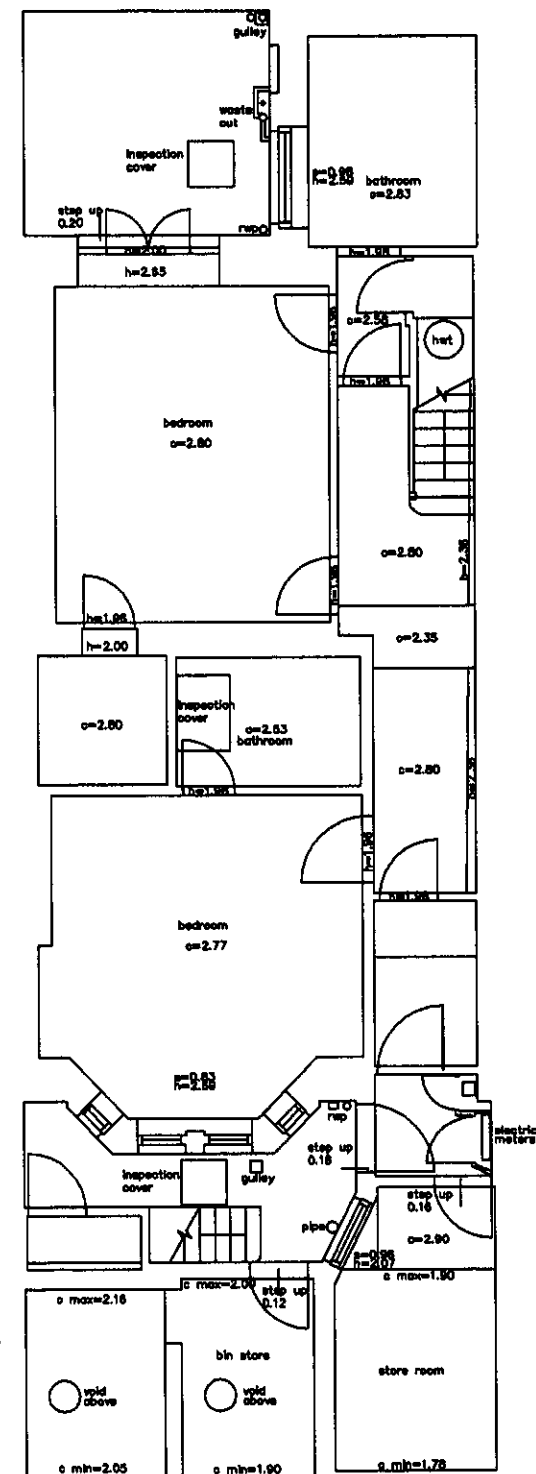

BASEMENT

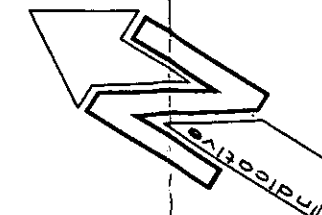

BUILDING CONSULTANCY
DESIGN SERVICES, BUILDING SURVEYING,
PROJECT MANAGEMENT, COST CONSULTANCY

Savills

Savills
25 Finsbury Circus,
London EC2M 7EE

Tel +44 (0) 20 7400 8644
Fax +44 (0) 20 7454 1333
www.savills.com

Project
24 HORNTON STREET
KENSINGTON, LONDON


Drawing
EXISTING LAYOUTS
BASEMENT AND GROUND FLOOR

Date 08/03/07	Scale 1:50 @ A1
Drawn By AB	Checked By JG
Drawing No. 45367	Rev.
	01

[illegible]



Location Plan Scale 1:1250

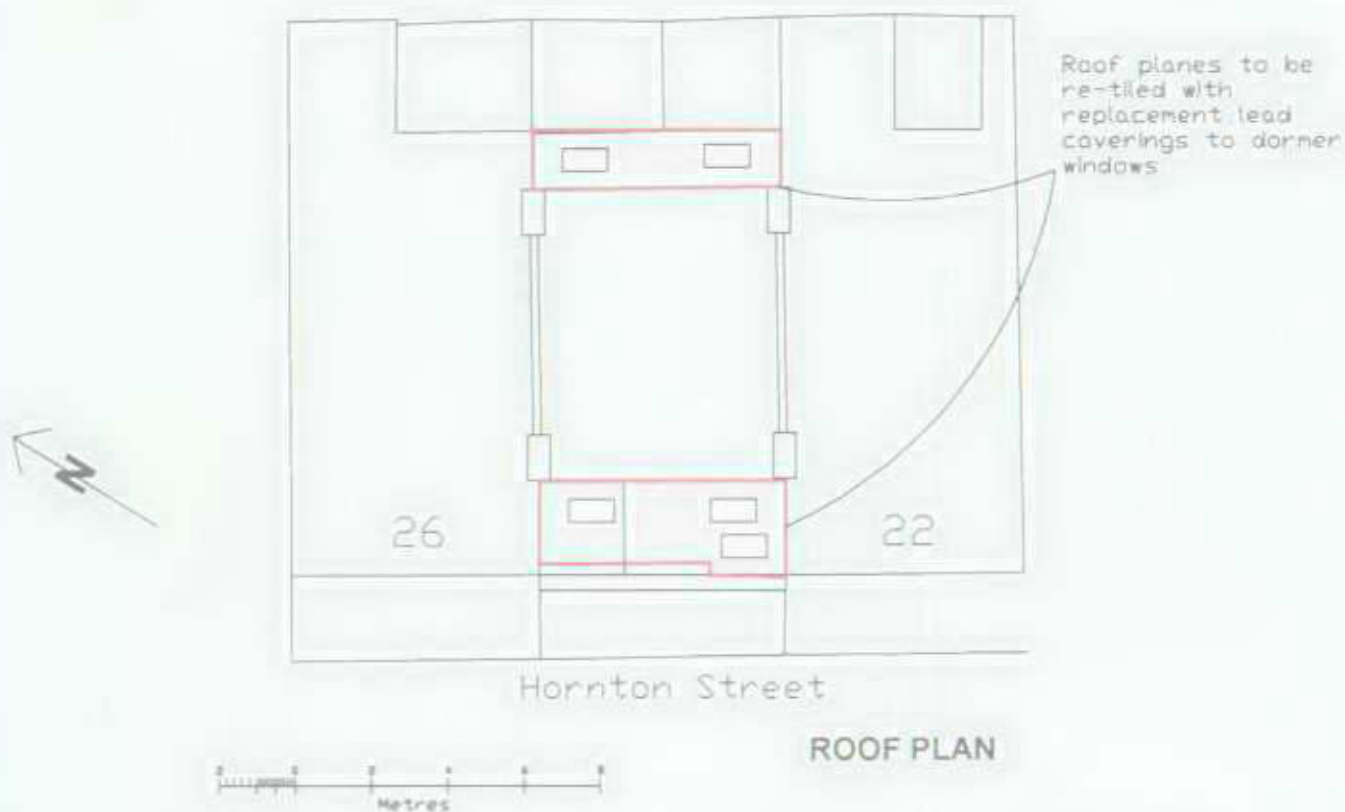

ROOF PLAN

Address 24 Hornton Street London W8 4NR	Client Phillimore 1984 Settlement Title Roof Plan and Location Plan	Date April 2007 Drawing No 04	Scale 1:200 @ A4 Rev /	BUILDING CONSULTANCY BUILDING SERVICES, BUILDING SURVEILLANCE, PROJECT MANAGEMENT, COST CONSULTANTS savills Savills 20 Finsbury Circus, 1st Floor, London EC2M 7EE Tel: +44 (0) 20 7499 8000 Fax: +44 (0) 20 7499 1333 www.savills.com
---	--	--	---	--


Legend



Walls to be treated for damp



Pavement vaults to be tanked

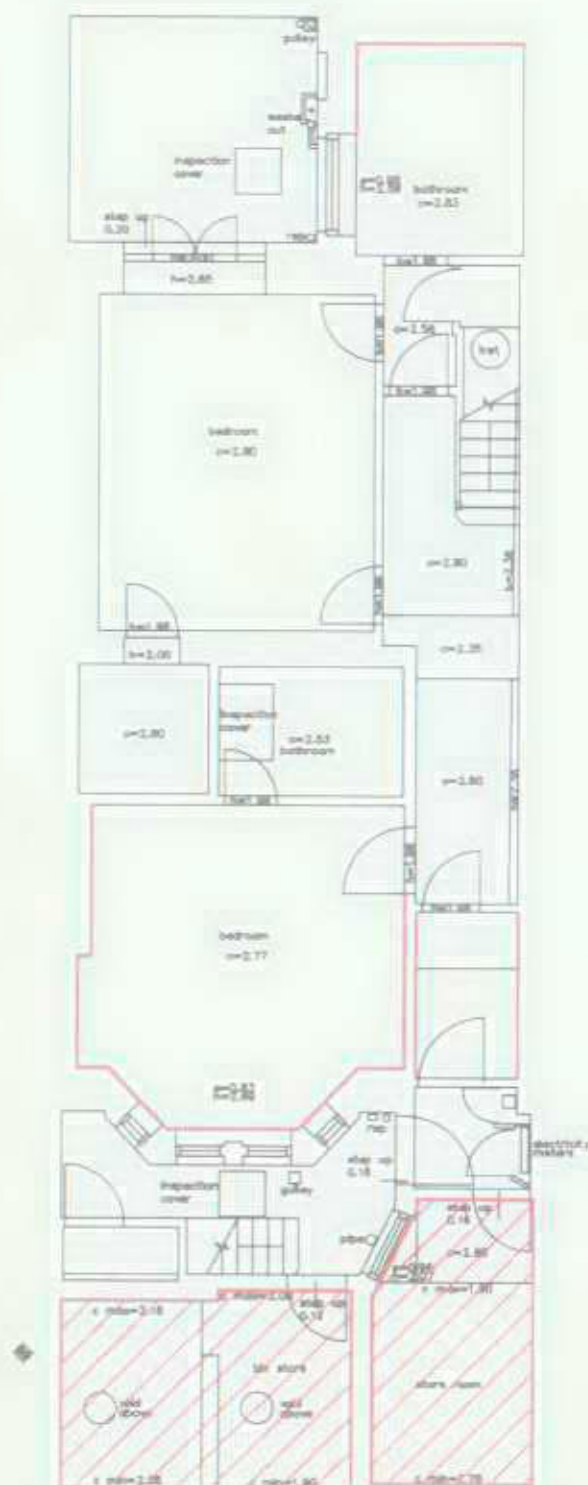

BASEMENT



BUILDING CONSULTANCY
 SERVICE SERVICES BUILDING SURVEYING
 PROJECT MANAGEMENT COST CONSULTANCY

Savills

Savills
 25 Finsbury Circus,
 London EC2M 7EE

Tel: +44 (0) 20 7438 8044
 Fax: +44 (0) 20 7438 1333
 www.savills.com

Project
 24 HORNTON STREET
 KENSINGTON, LONDON

Building
 DAMP PROOF WORKS TO THE
 BASEMENT LEVEL

Date 10/04/07	Scale 1:50	@ A4
Drawn By RH	Checked By	
Building No.		Rev.
	05	

Appendix 3: Schedule of Photographs

2.1 Renewal of roof coverings to main roof



Photo 1
Front
elevation



Photo 2
Rear
Elevation



Photo 3
Previously
repaired roof
tiles



Photo 4
Redland Plain
tiles from the
Rosemary
Classic range,
type 81 Light
Mixed Brindle
Smooth

2.2 Basement Damp Proofing Works

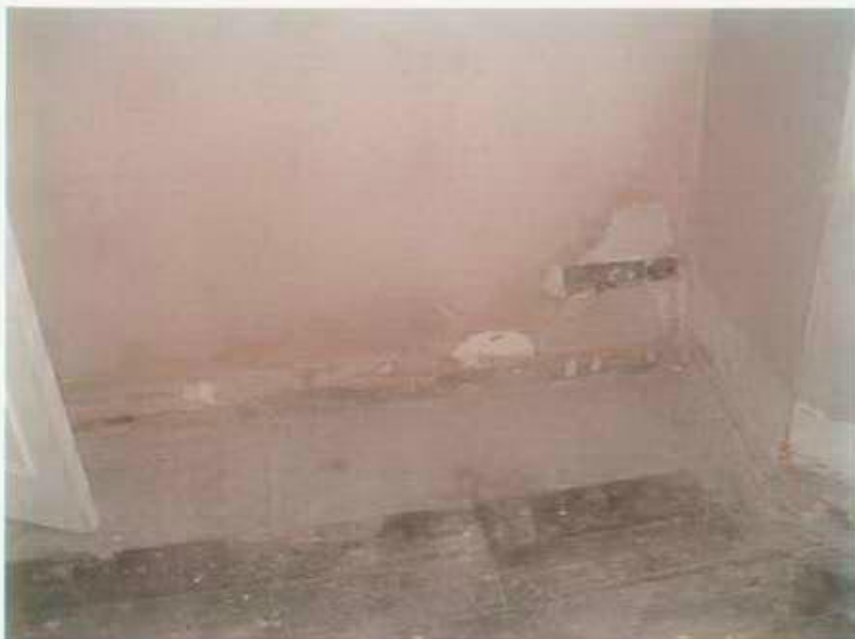


Photo 5
Damp to the
front Bedroom



Photo 6
Damp to the
rear bathroom