




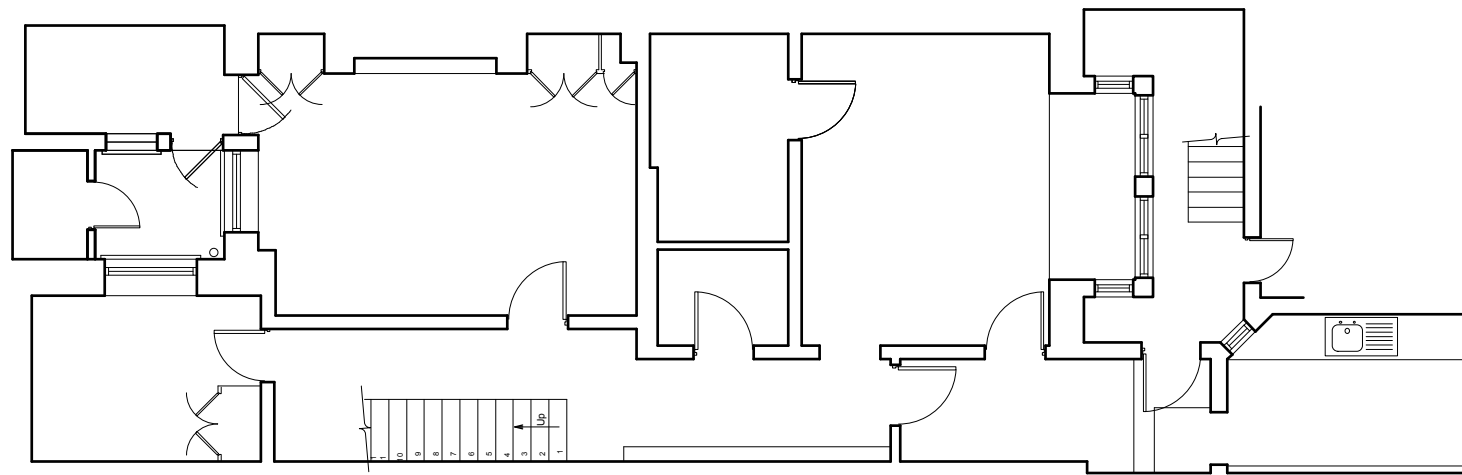

1 Existing Basement Plan
Scale: 1:100

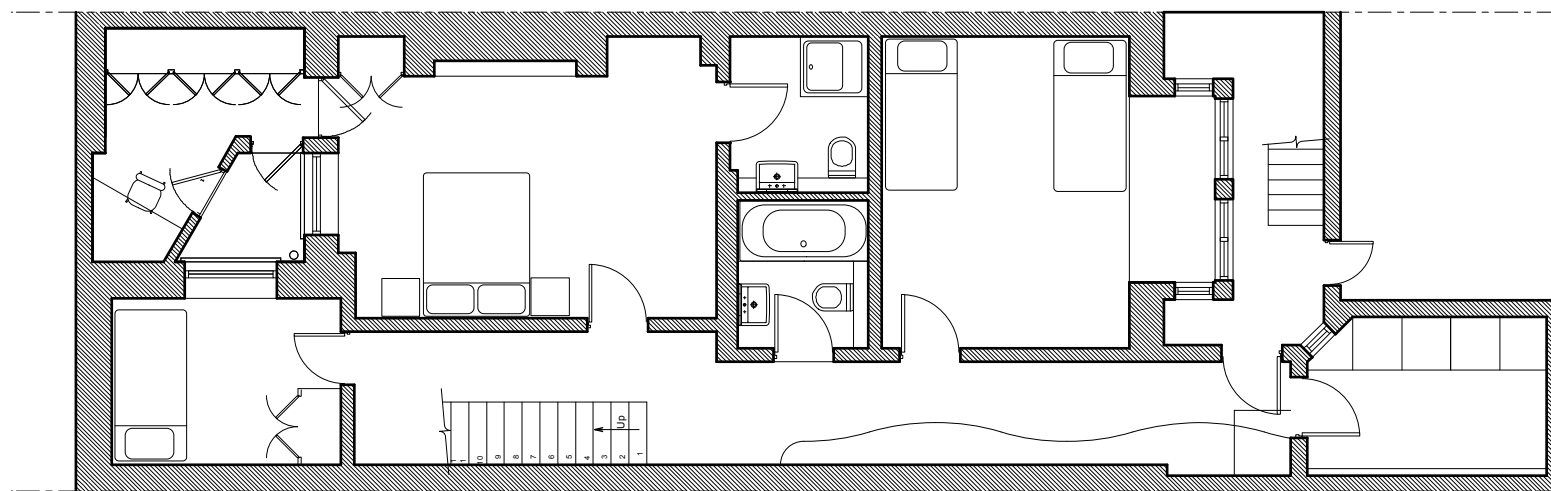

2 Previously Approved Basement Plan
Scale: 1:100

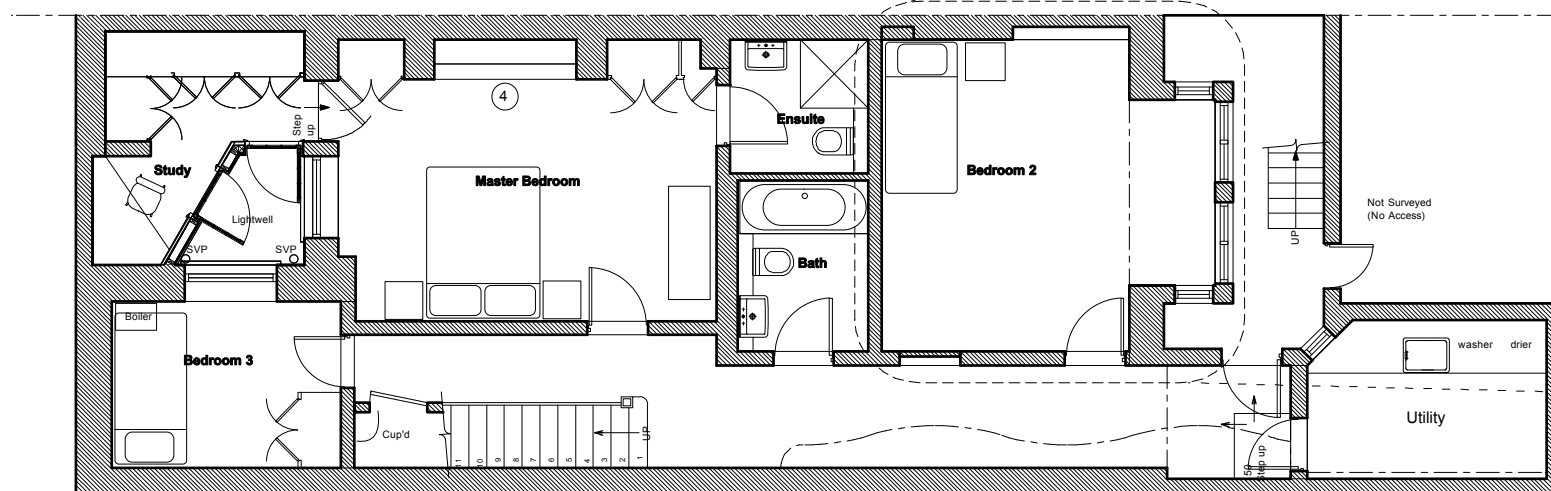

3 Proposed Basement Plan
Scale: 1:100


0 1m 2 3 4 5m

0 1m 2 3 4 5m

NOTE: DO NOT SCALE OFF THIS DRAWING
ALL DIMS TO BE CHECKED ON SITE


notes:

1. Block up door opening ; plaster and paint to match existing wall. Remove architrave and reinstall on adjacent door (2). Retain recess for bookshelf.
2. Replace architrave with architrave removed from adjacent doorway.
3. False wall to be removed adjacent to chimney breast. Timber painted shelves to be installed. Existing cornice and skirting retained.
4. Unblock existing fireplace recess.

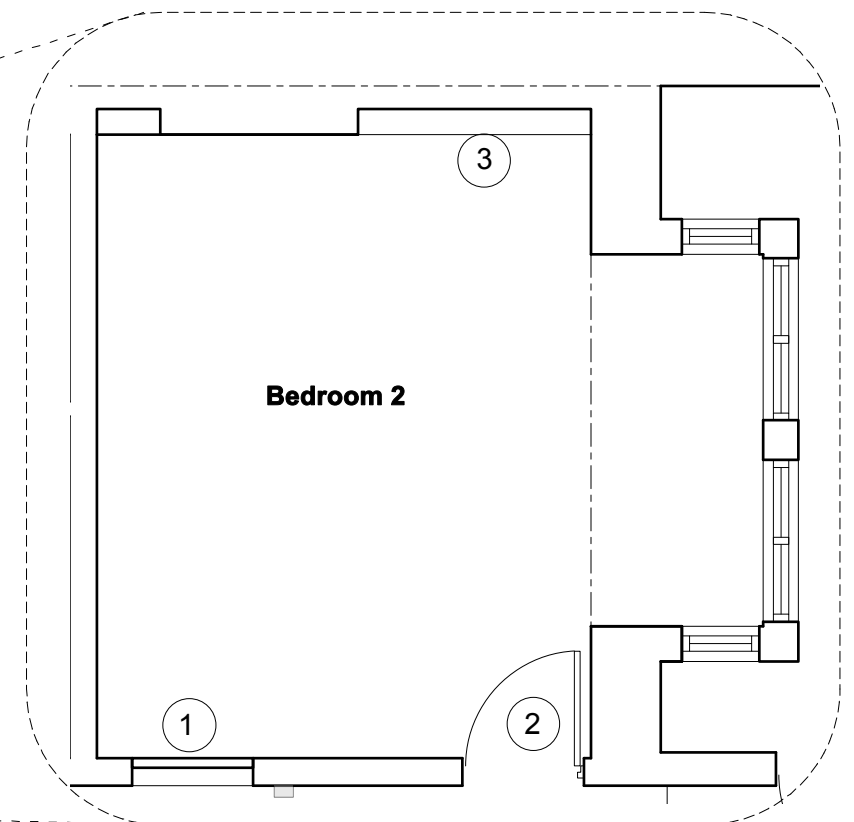


4 Proposed Bedroom 2 Plan
Scale: 1:50


revision notes :		date of revision :		rev no. :
raw space info@rawspace.co.uk 02087 417 341 London W6 9TA		site :	30 Hornton Street	
		drawing title :	Basement Floorplan	
client :		cad file name :	664 Master 160414.vwx	
		project id :	664	sheet no. : .001
		date :	4/6/14	
		scale :	1:100/50 @ A3	
		drawing no. :	104	

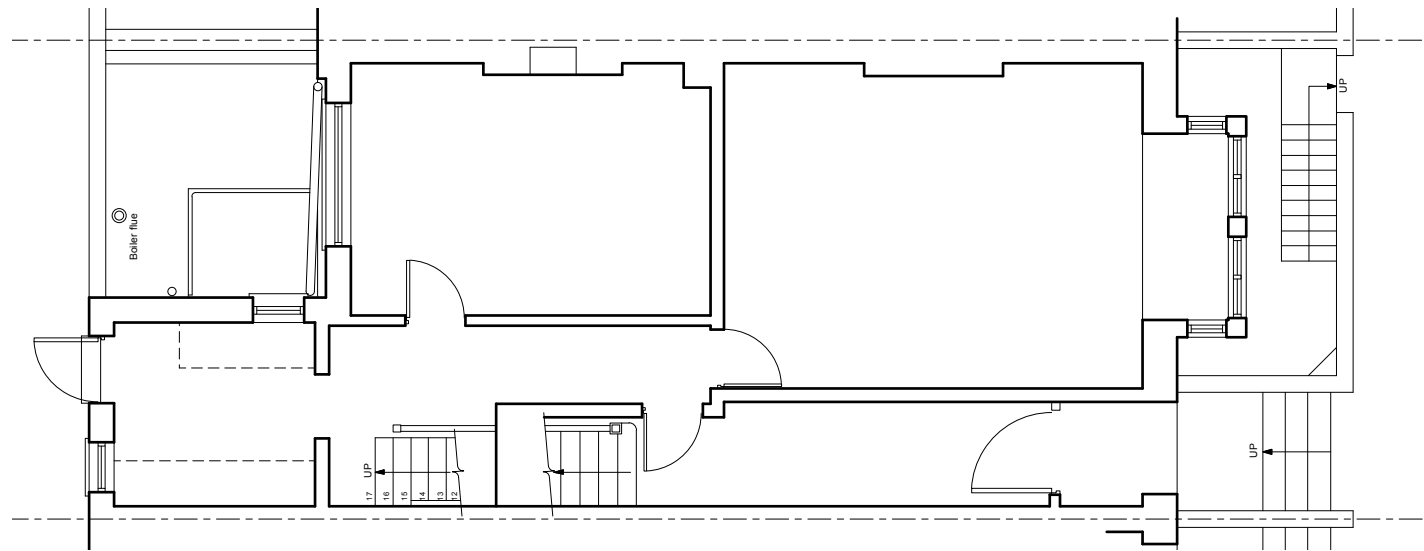

5 As Existing Plans
Scale: 1:100

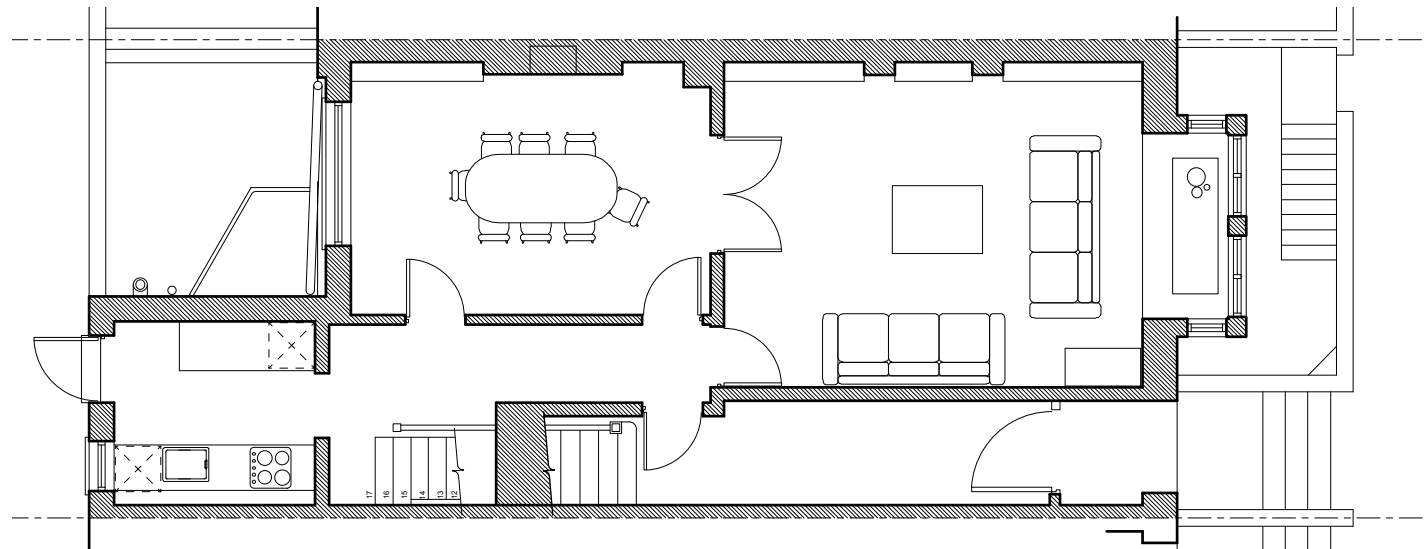


6 Previously Approved Groundfloor Plan
Scale: 1:20

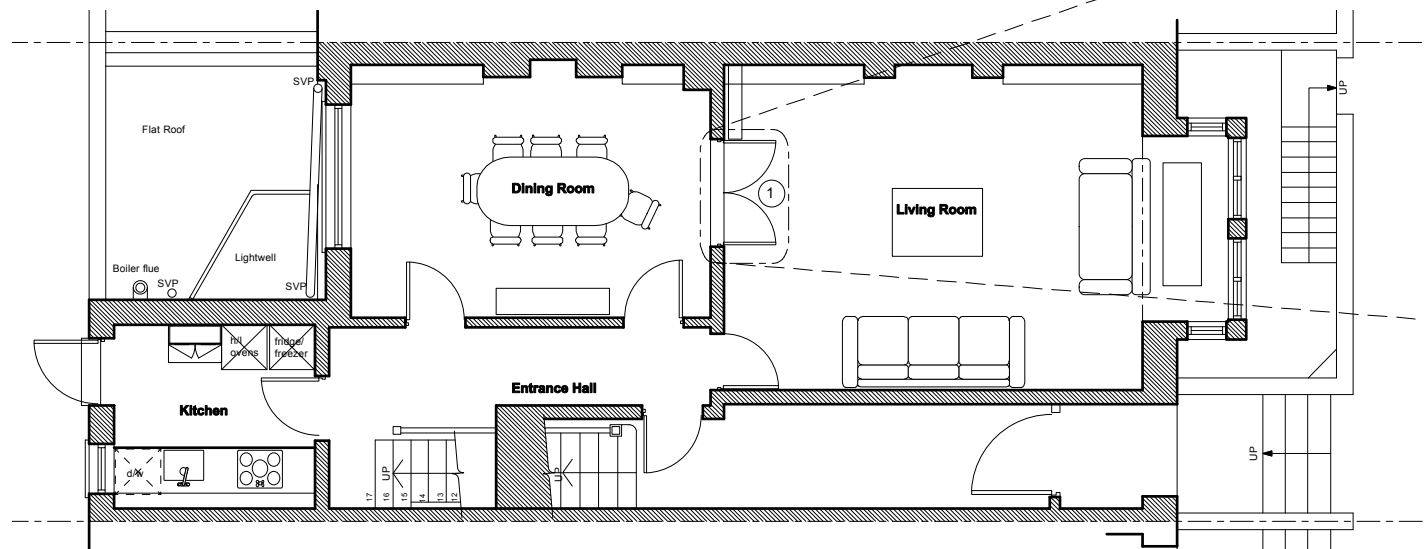

7 Proposed Plans
Scale: 1:100

notes:

1. Amend width of new opening to match width of historic opening found.

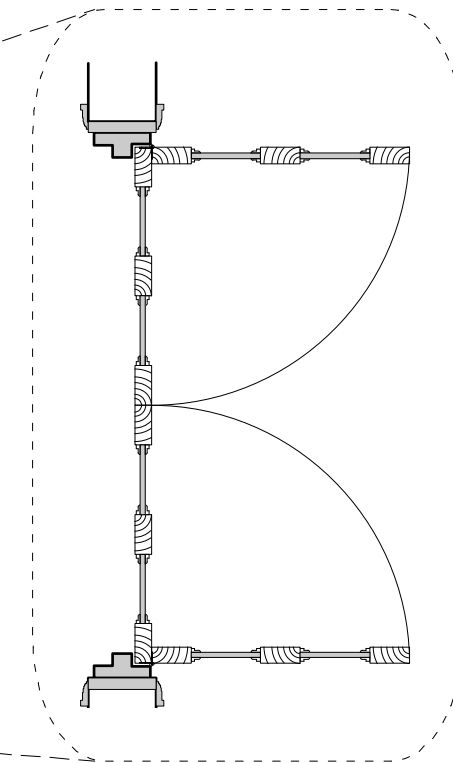


8 Proposed Door Detail
Scale: 1:20


NOTE: DO NOT SCALE OFF THIS DRAWING
ALL DIMS TO BE CHECKED ON SITE



revision notes :		date of revision :	rev no. :
rawspace info@rawspace.co.uk 02087 417 341 London W6 9TA		site :	30 Hornton Street
		drawing title :	Ground Floorplan
client : Lorcan & Helena O'Shea		cad file name :	664 Master 160414.vwx
		scale :	1:100/20 @ A3
project id :	664	drawing no. :	104
sheet no. :			.002

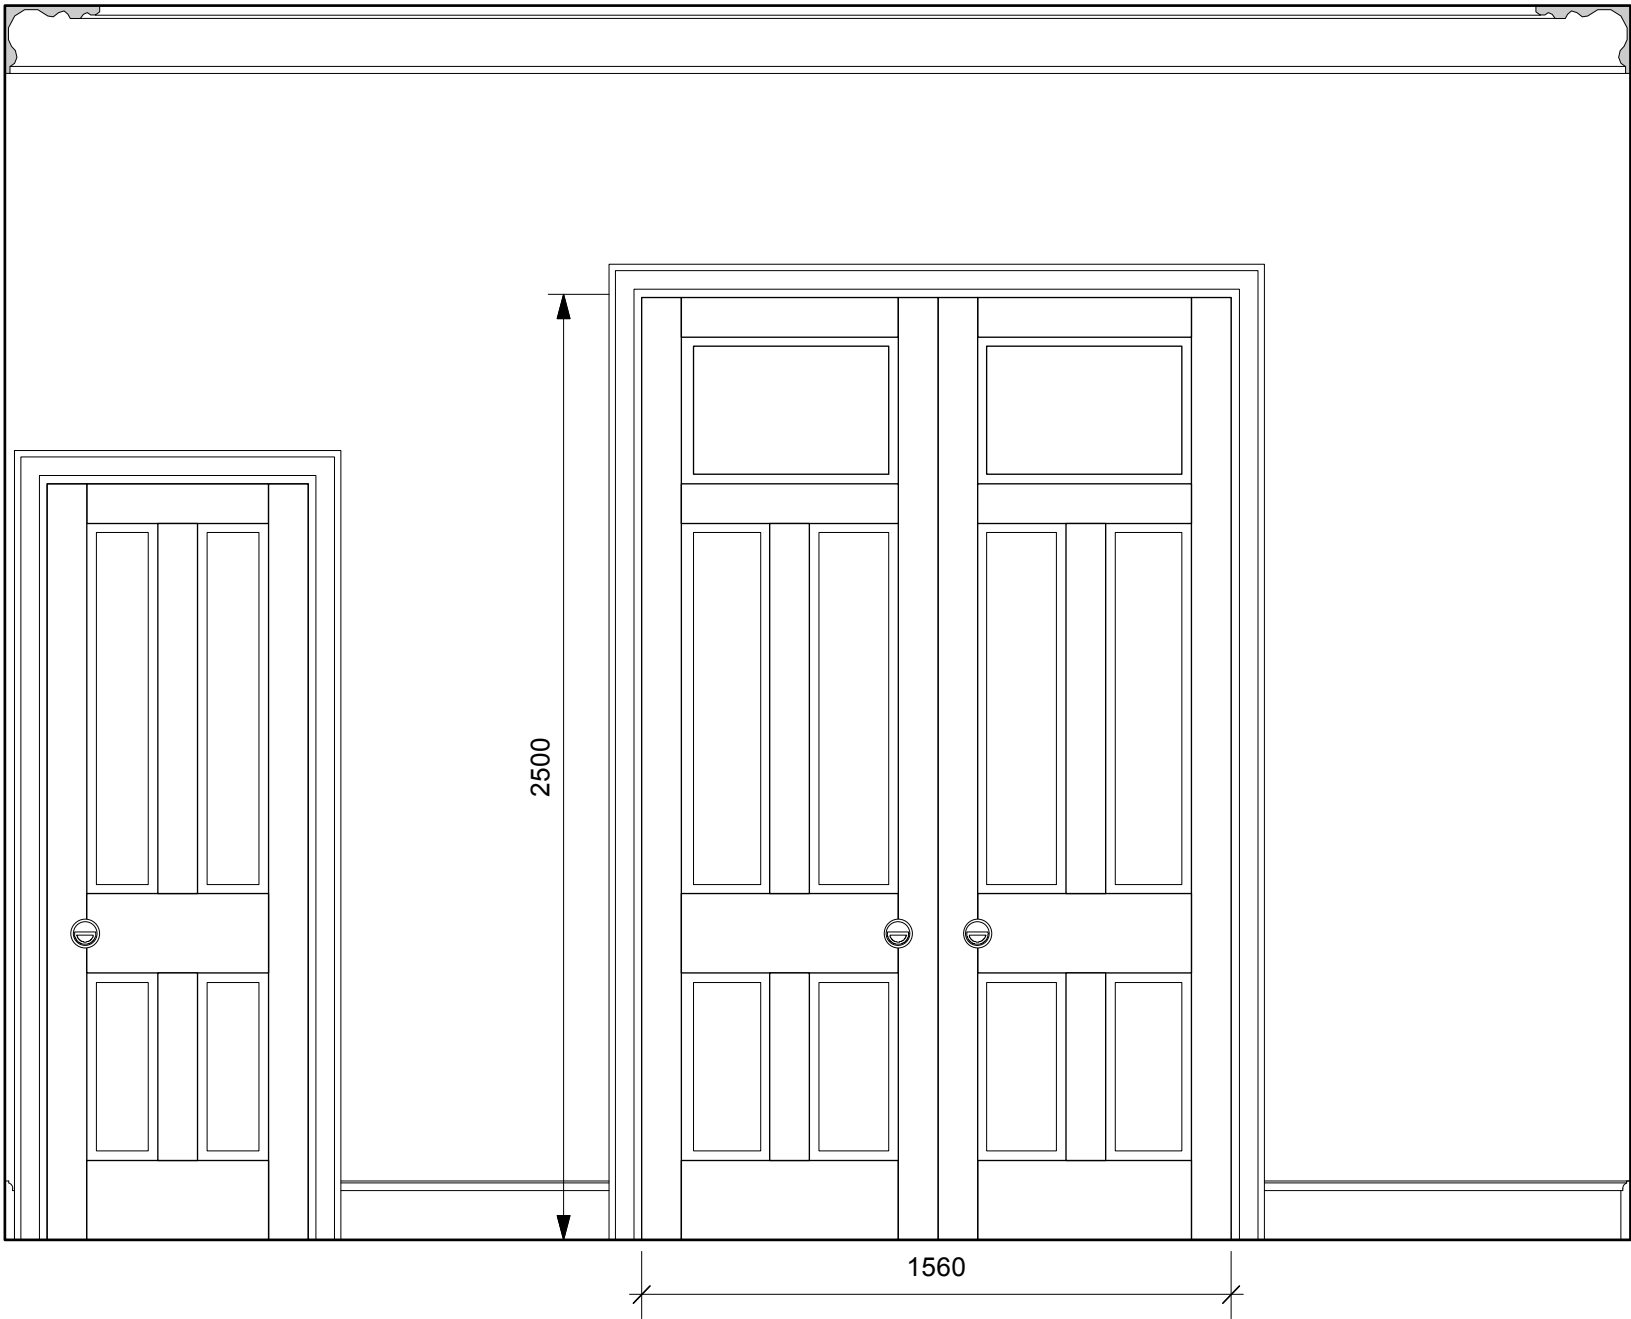


9 Previously Approved Door Elevation from Living Room
Scale: 1:20

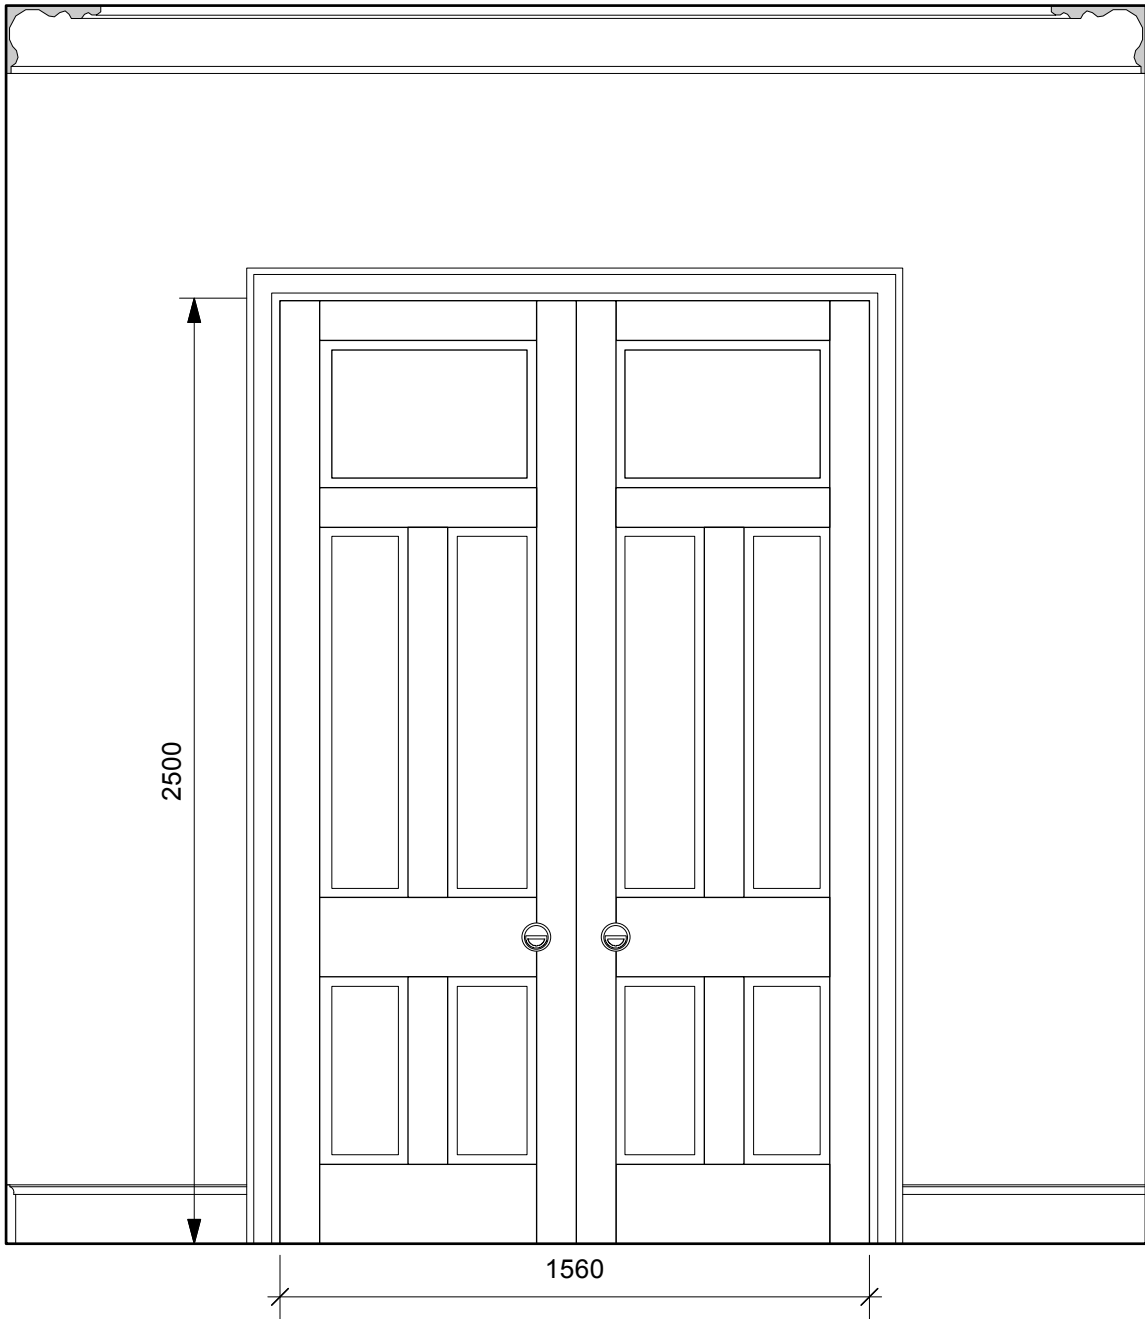


10 Previously Approved Door Elevation from Sitting Room
Scale: 1:20


NOTE: DO NOT SCALE OFF THIS DRAWING
ALL DIMS TO BE CHECKED ON SITE

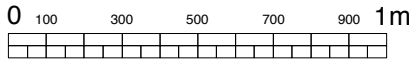

revision notes :			date of revision :	rev no. :
raw space info@rawspace.co.uk 02087 417 341 London W6 9TA			date : 4/6/14 scale : 1:20 @ A3 project id : 664	rev no. : sheet no. : 104 .003
site : 30 Hornton Street		drawing title : Internal Elevations		
client : Lorcan & Helena O'Shea		cad file name : 664 Master 160414.vwx		

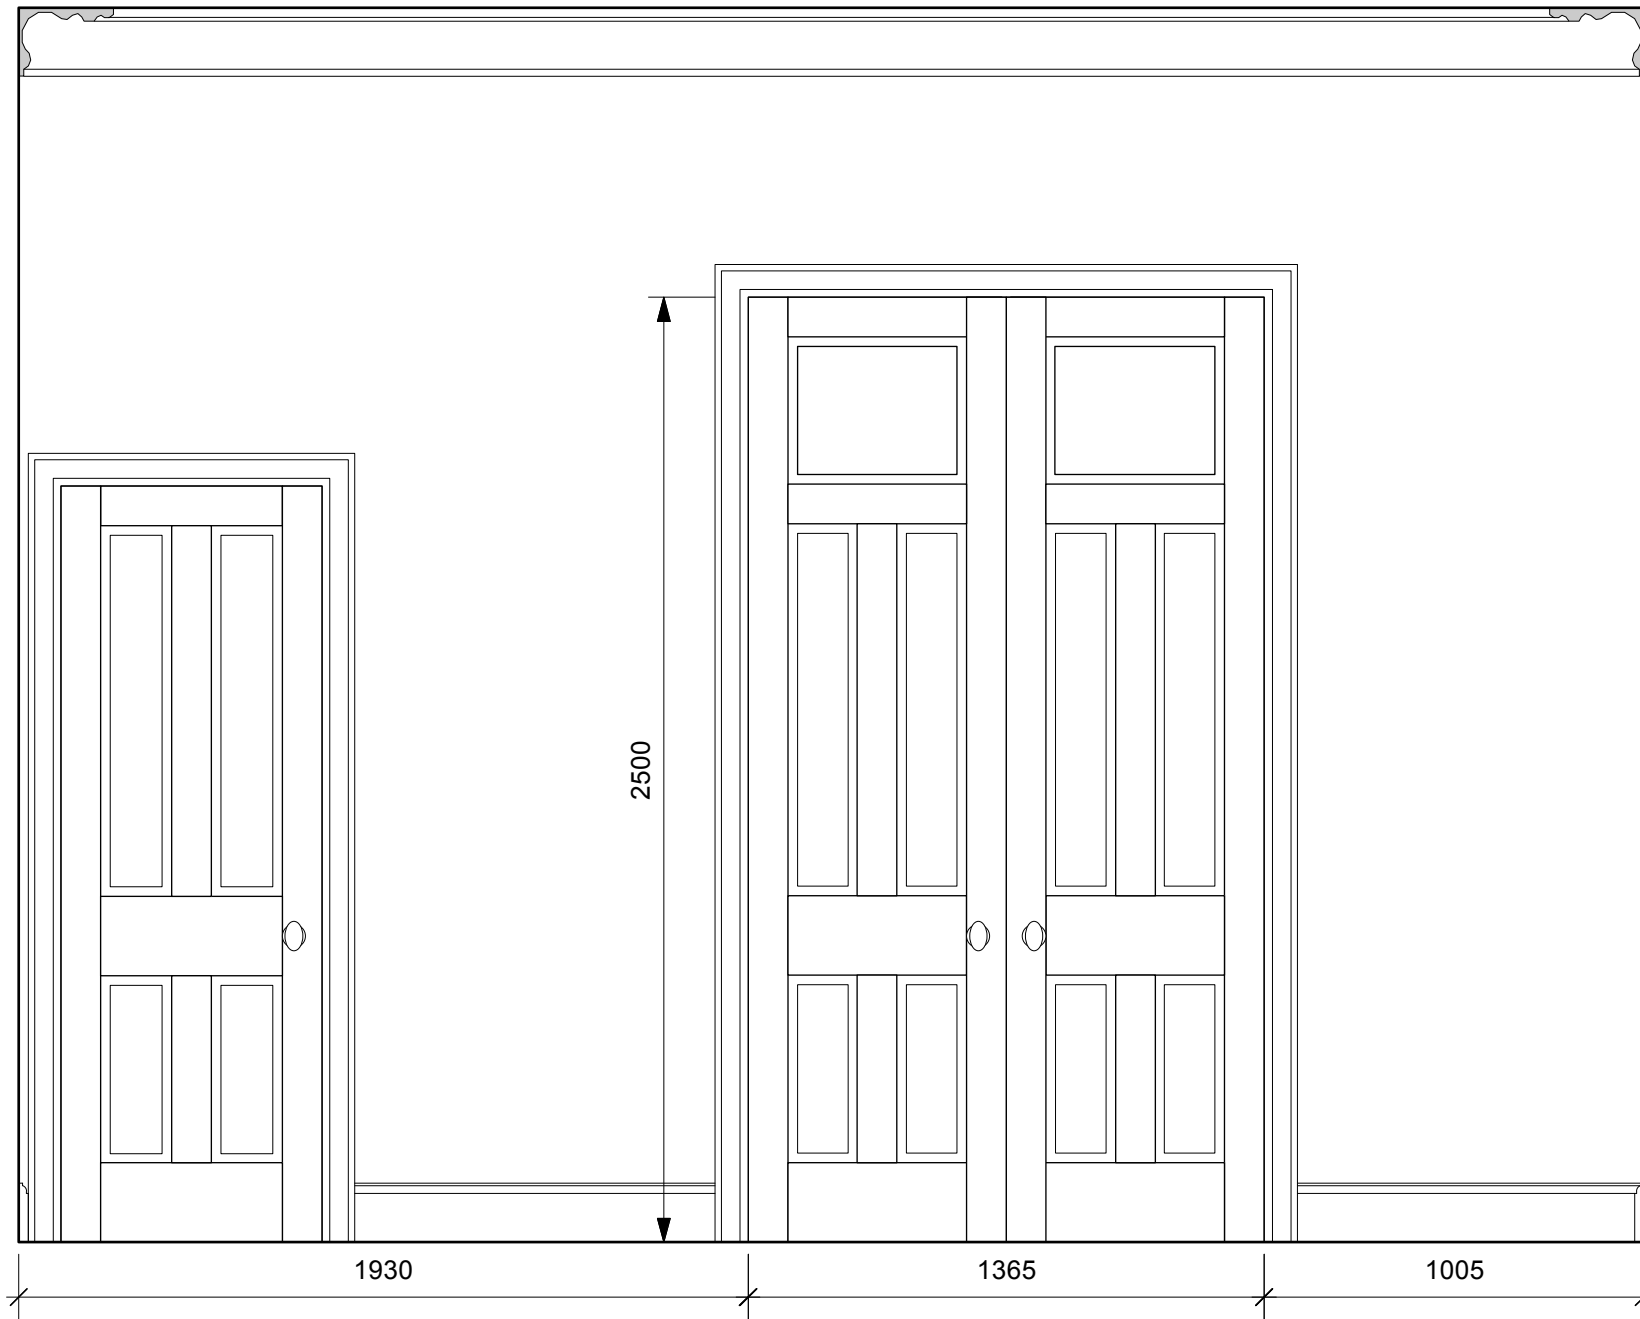


11 Proposed Door Elevation from Living Room
Scale: 1:20

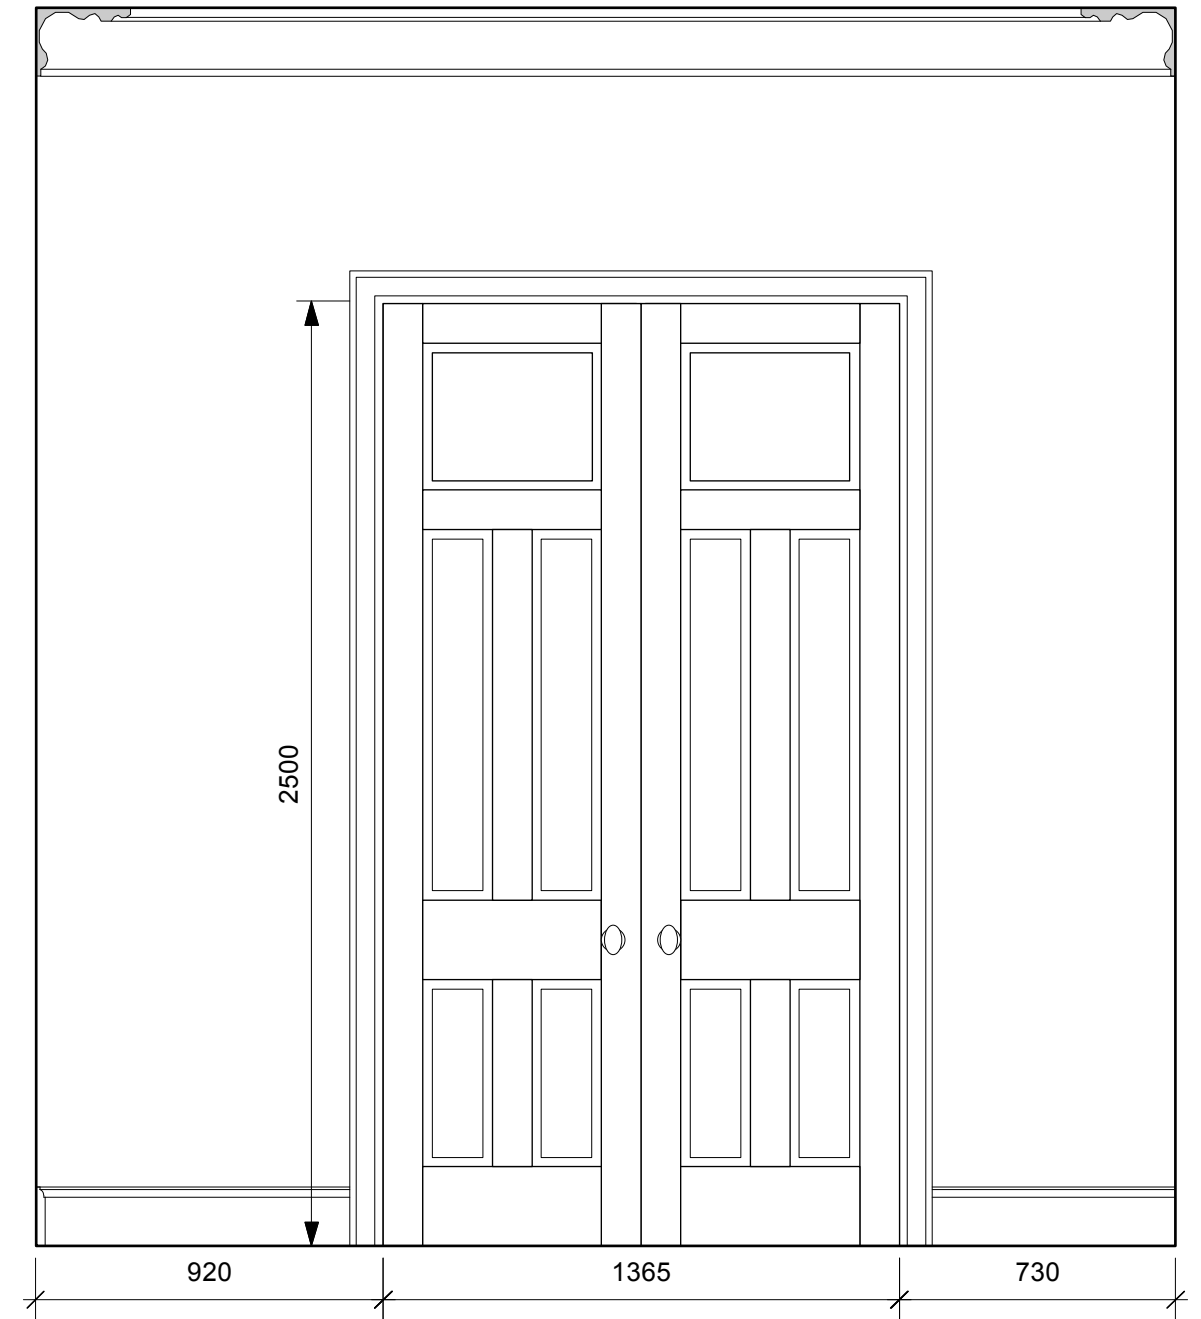

12 Proposed Door Elevation from Sitting Room
Scale: 1:20

NOTE: DO NOT SCALE OFF THIS DRAWING
ALL DIMS TO BE CHECKED ON SITE

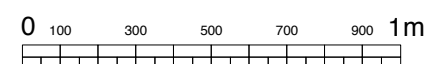

revision notes :			date of revision :		rev no. :
raw space info@rawspace.co.uk 02087 417 341 London W6 9TA			site :		30 Hornton Street
			drawing title :		Internal Elevations
			client :		Lorcan & Helena O'Shea
			cad file name :		664 Master 160414.vwx
			date :	4/6/14	
			scale :	1:20 @ A3	
			project id :	drawing no. :	sheet no. :
			664	104	.004