



ELEVATION (developed)

Treads side-projected from centre pole.

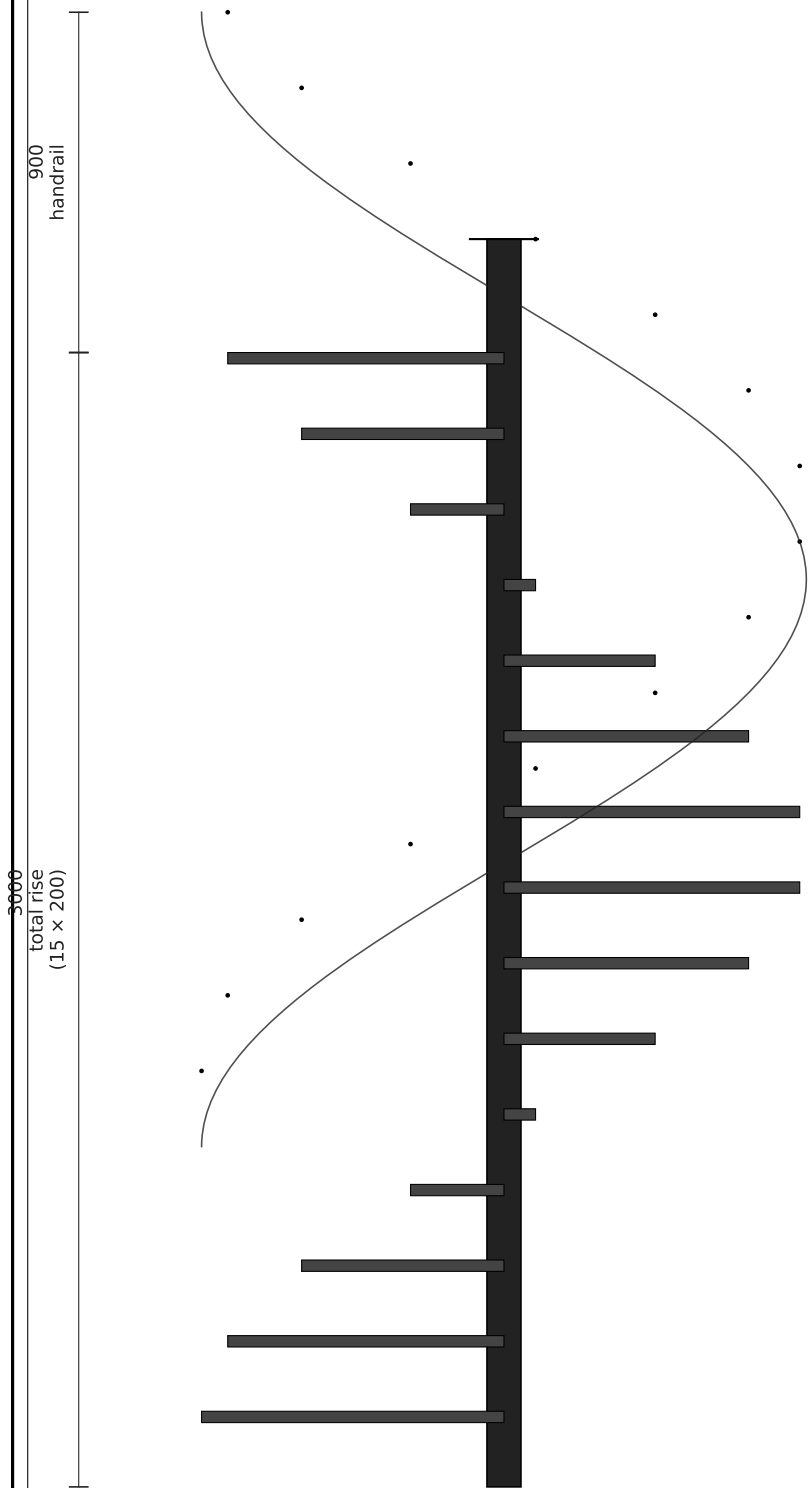

PLAN (top-down footprint)

Viewed from above; tread numbers shown.

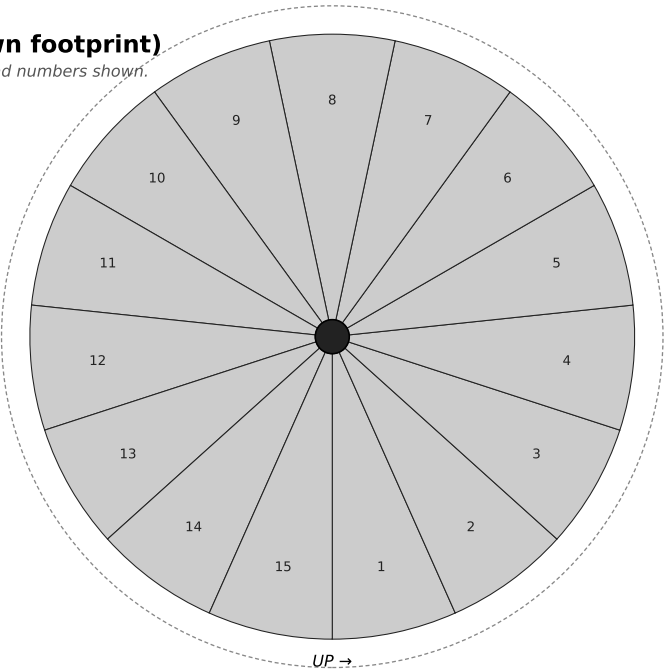

SCHEDULE

Risers:	15 (15 risers fitting 3000 mm Rise)
Rise per tread:	200 mm (200-210 verified on artefact)
Total rise:	3000 mm
Central pole height:	3300 mm
Pole diameter:	90 mm
Outer radius (tread):	800 mm
Envelope diameter:	1750 mm (~175 cm)
Tread widest dim:	340 mm
Tread thickness:	30 mm
Rotation/tread:	24°
Handrail height:	900 mm above tread
Finish:	dark painted cast iron

INSTALLATION

- Base plate bolted to courtyard slab (engineer-designed).
- Top tread / landing-pad lands at new kitchen-doorway threshold (= GF FFL above courtyard slab).
- Pole top above handrail — cap to match Victorian newel.
- Side-fixed to side wall via 2 brackets + propped off pole.
- Final structural detail by engineer; installer to verify achievable rise vs. measured site dim; landing-pad spacer to take up tolerance up to ±25 mm.

PROJECT	Flat 1, 20 Hornton Street, London W8 4NR	SCALE	1:20 @ A3
DRAWING TITLE	SPIRAL STAIRCASE — Plan & Elevation Detail (1:20)	DRAWING NO.	06
CLIENT	Grahame McGirr	DATE	2026-05-25
REVISION	B	SHEET SIZE	A3 (420 x 297)
UNITS	All dimensions in millimetres (mm)	STATUS	FOR PLANNING

Scale 1:20

